




DEMOLITION DESCRIPTION		
CODE	SYMBOL	DESCRIPTION
		Remove existing bar counter
		Remove all existing walls
		Remove existing floor

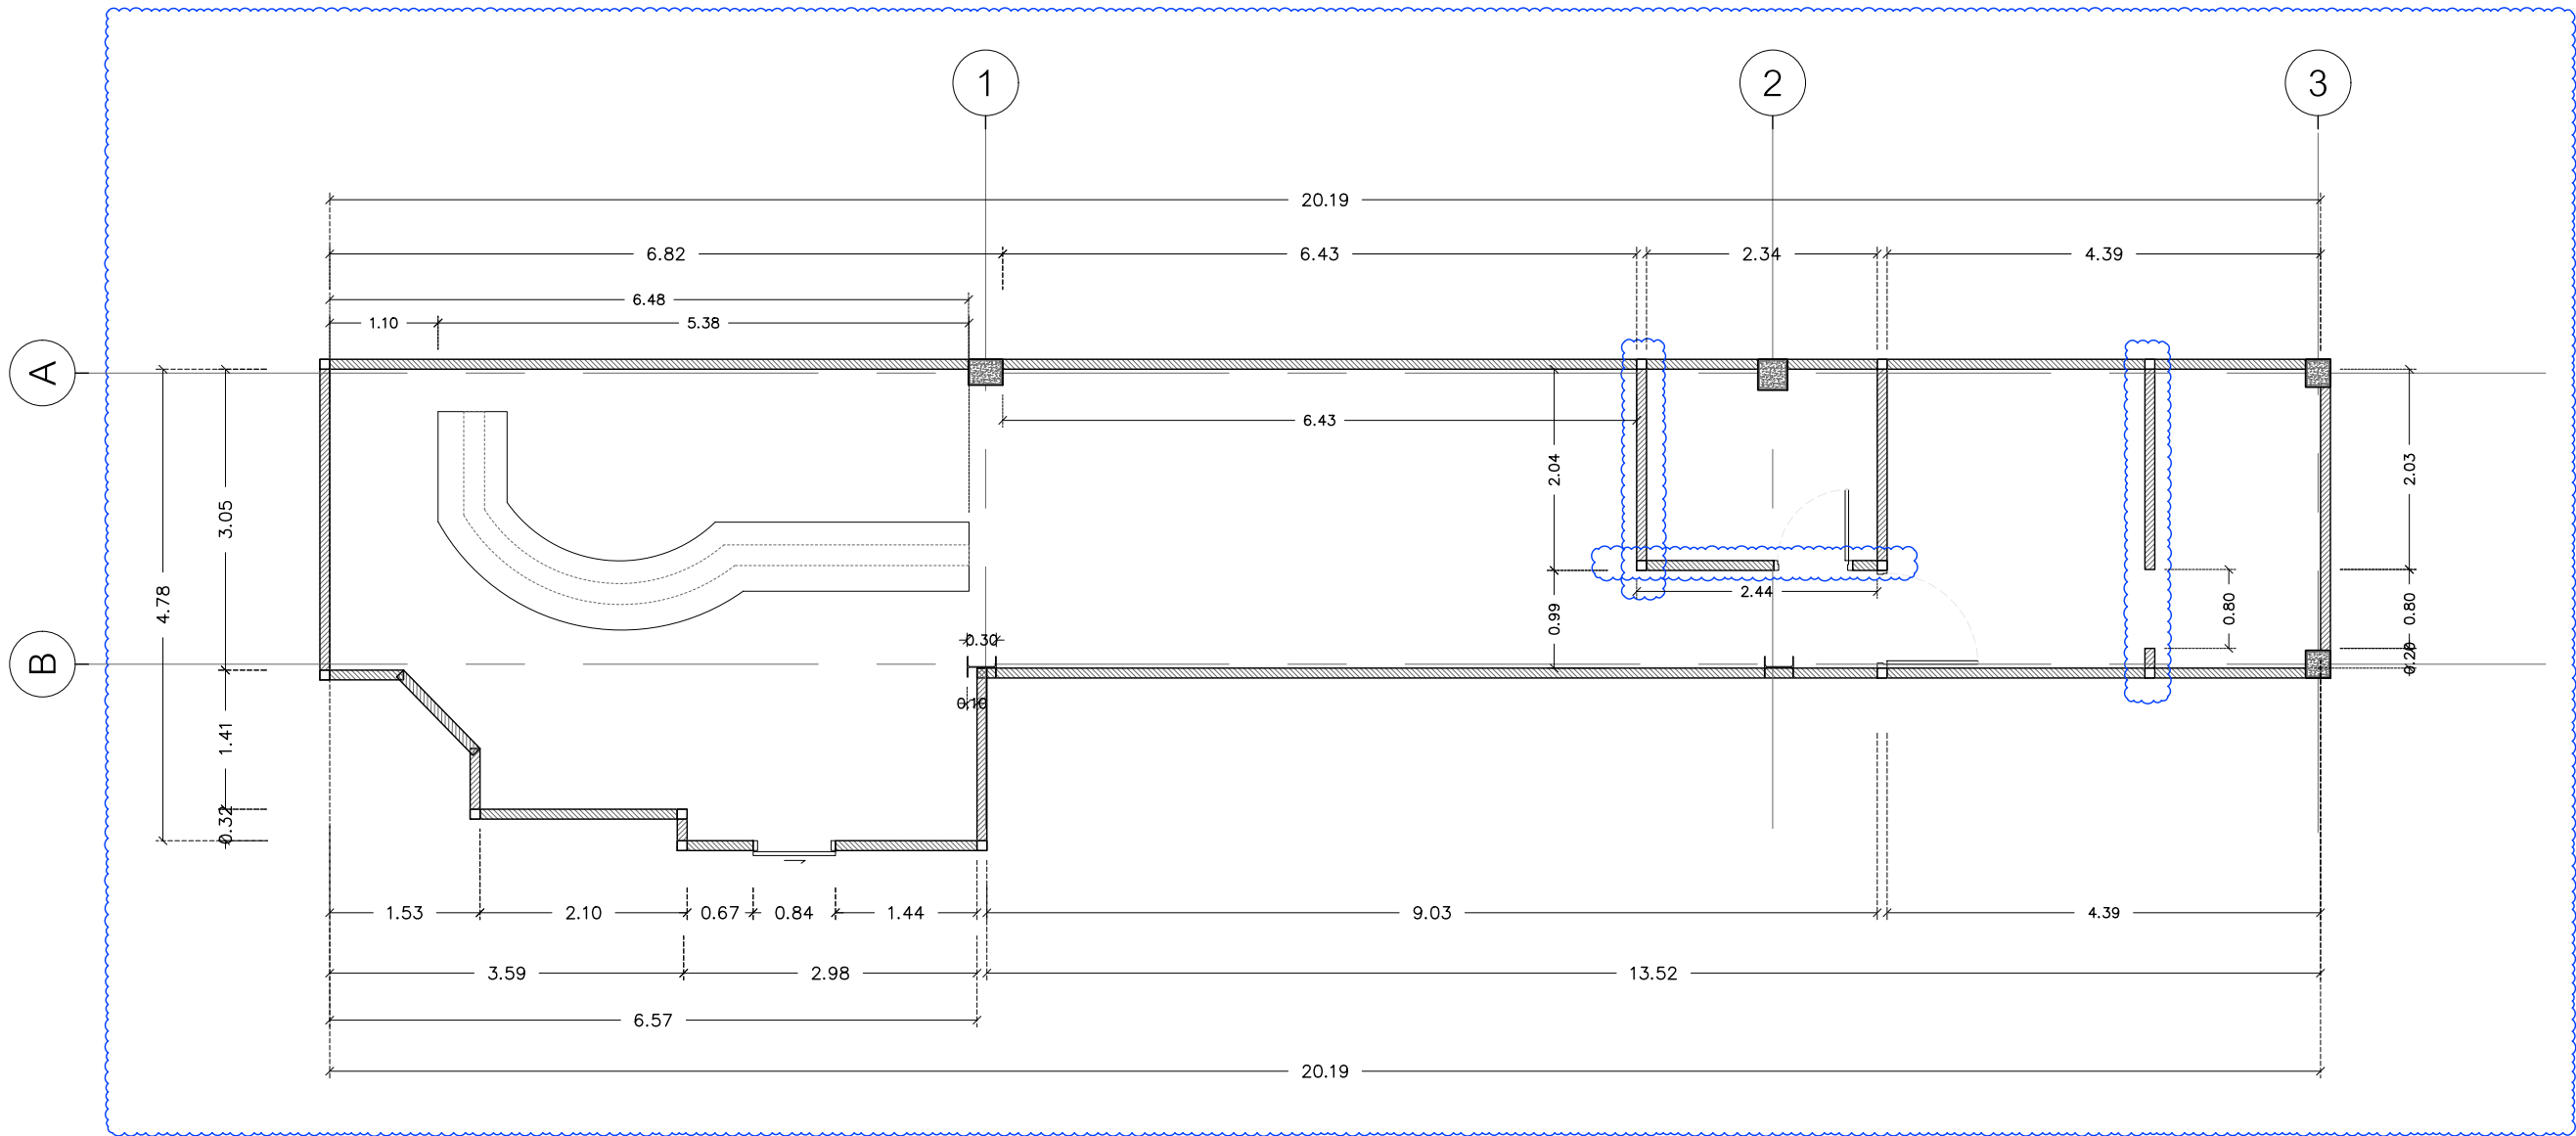

DEMOLITION LAYOUT PLAN

SCALE 1 : 75

PROJECT TITLE

OWNER

ARCHITECTS

STRUCTURAL ENGINEERS

INTERIOR DESIGNER

DRAWN BY

DRAWING TITLE

SCALE 1:75

NOTE :

USE WRITTEN DIMENSION ONLY
ใช้คำตัวเลขที่กำหนดไว้เท่านั้น
ห้ามวัดจากแบบ
วัดพื้นที่ทุกครั้งก่อนดำเนินการ

NO	DATE	DESCRIPTION
----	------	-------------

DATE / / 2568

DRAWING No.	PAGE TOTAL
-------------	------------

A-

00



PROJECT TITLE

OWNER

ARCHITECTS

STRUCTURAL ENGINEERS

INTERIOR DESIGNER

DRAWN BY

DRAWING TITLE

SCALE 1:75

NOTE :


USE WRITTEN DIMENSION ONLY
ใช้เขียนตัวเลขที่กำหนดไว้เท่านั้น
ห้ามวัดจากแบบ
วัดพื้นที่ทุกห้องก่อนดำเนินการ

NO	DATE	DESCRIPTION

DATE / / 2568

DRAWING No. PAGE TOTAL.


A- 00

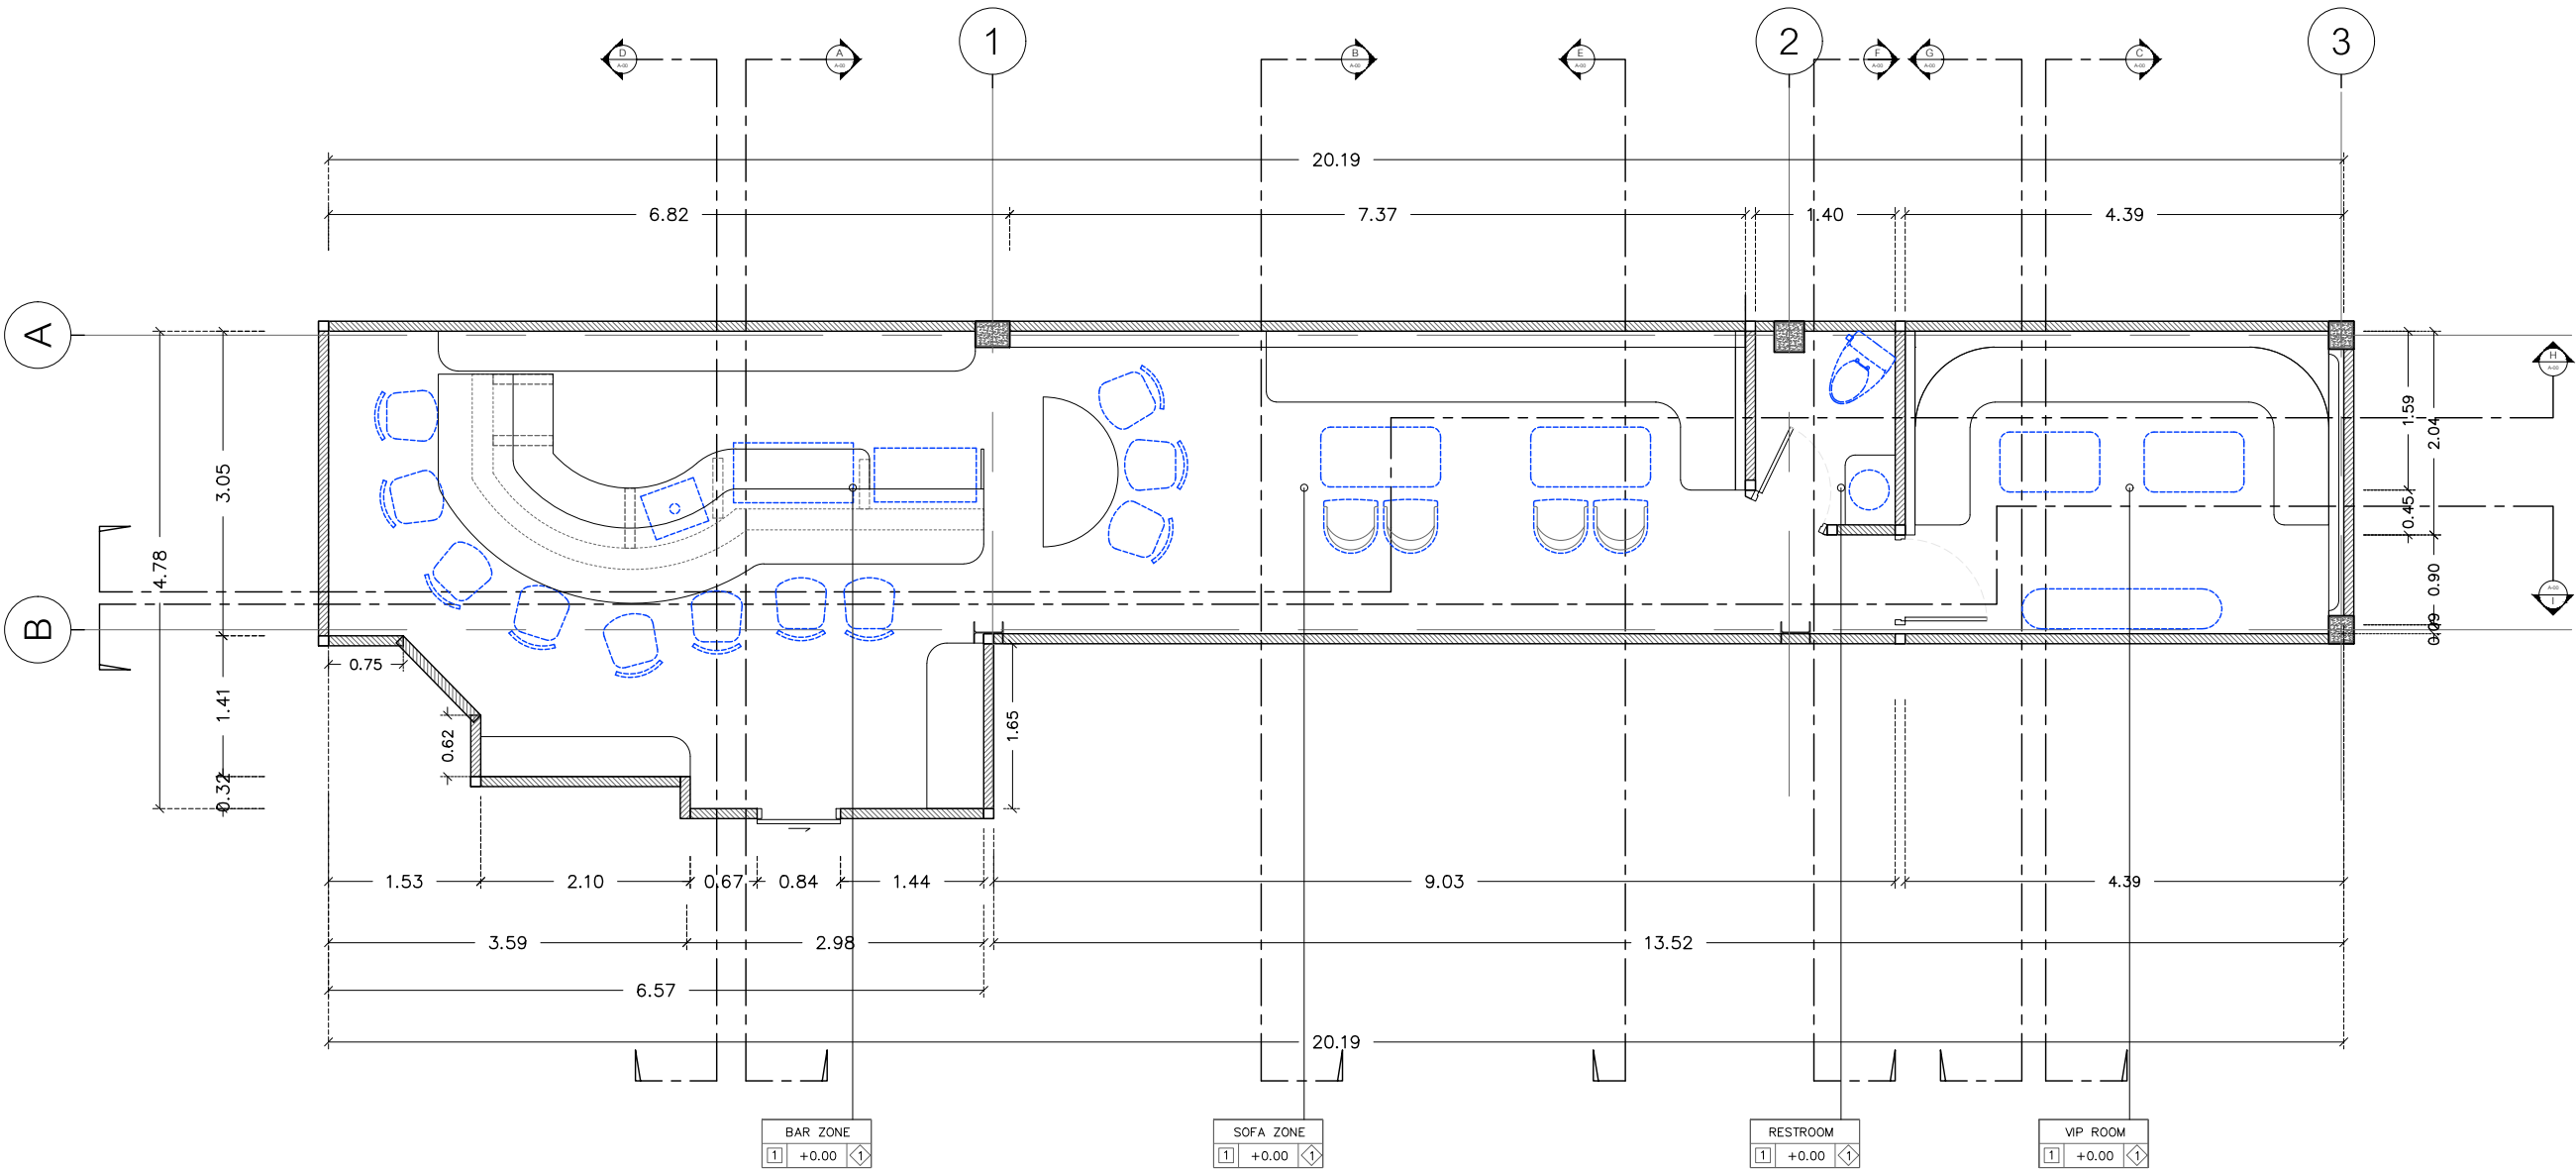

KEY PLAN

SCALE 1 : 75

FURNITURE		
CODE	SYMBOL	DESCRIPTION
F01		H 750 Counter seating เก้าอี้บาร์ (สตูลสูง 750)
F02		H 450 Chair เก้าอี้ (สูง 450)
F03		W 2000 D 500 H 850 Console Table โต๊ะ
F04		W 1200 D 600 H 450 TABLE โต๊ะ
F05		W 1000 D 600 H 450 TABLE โต๊ะ
F06		W 700 D 500 H 850 SINK
		The blue dashed line indicates items provide by the owner

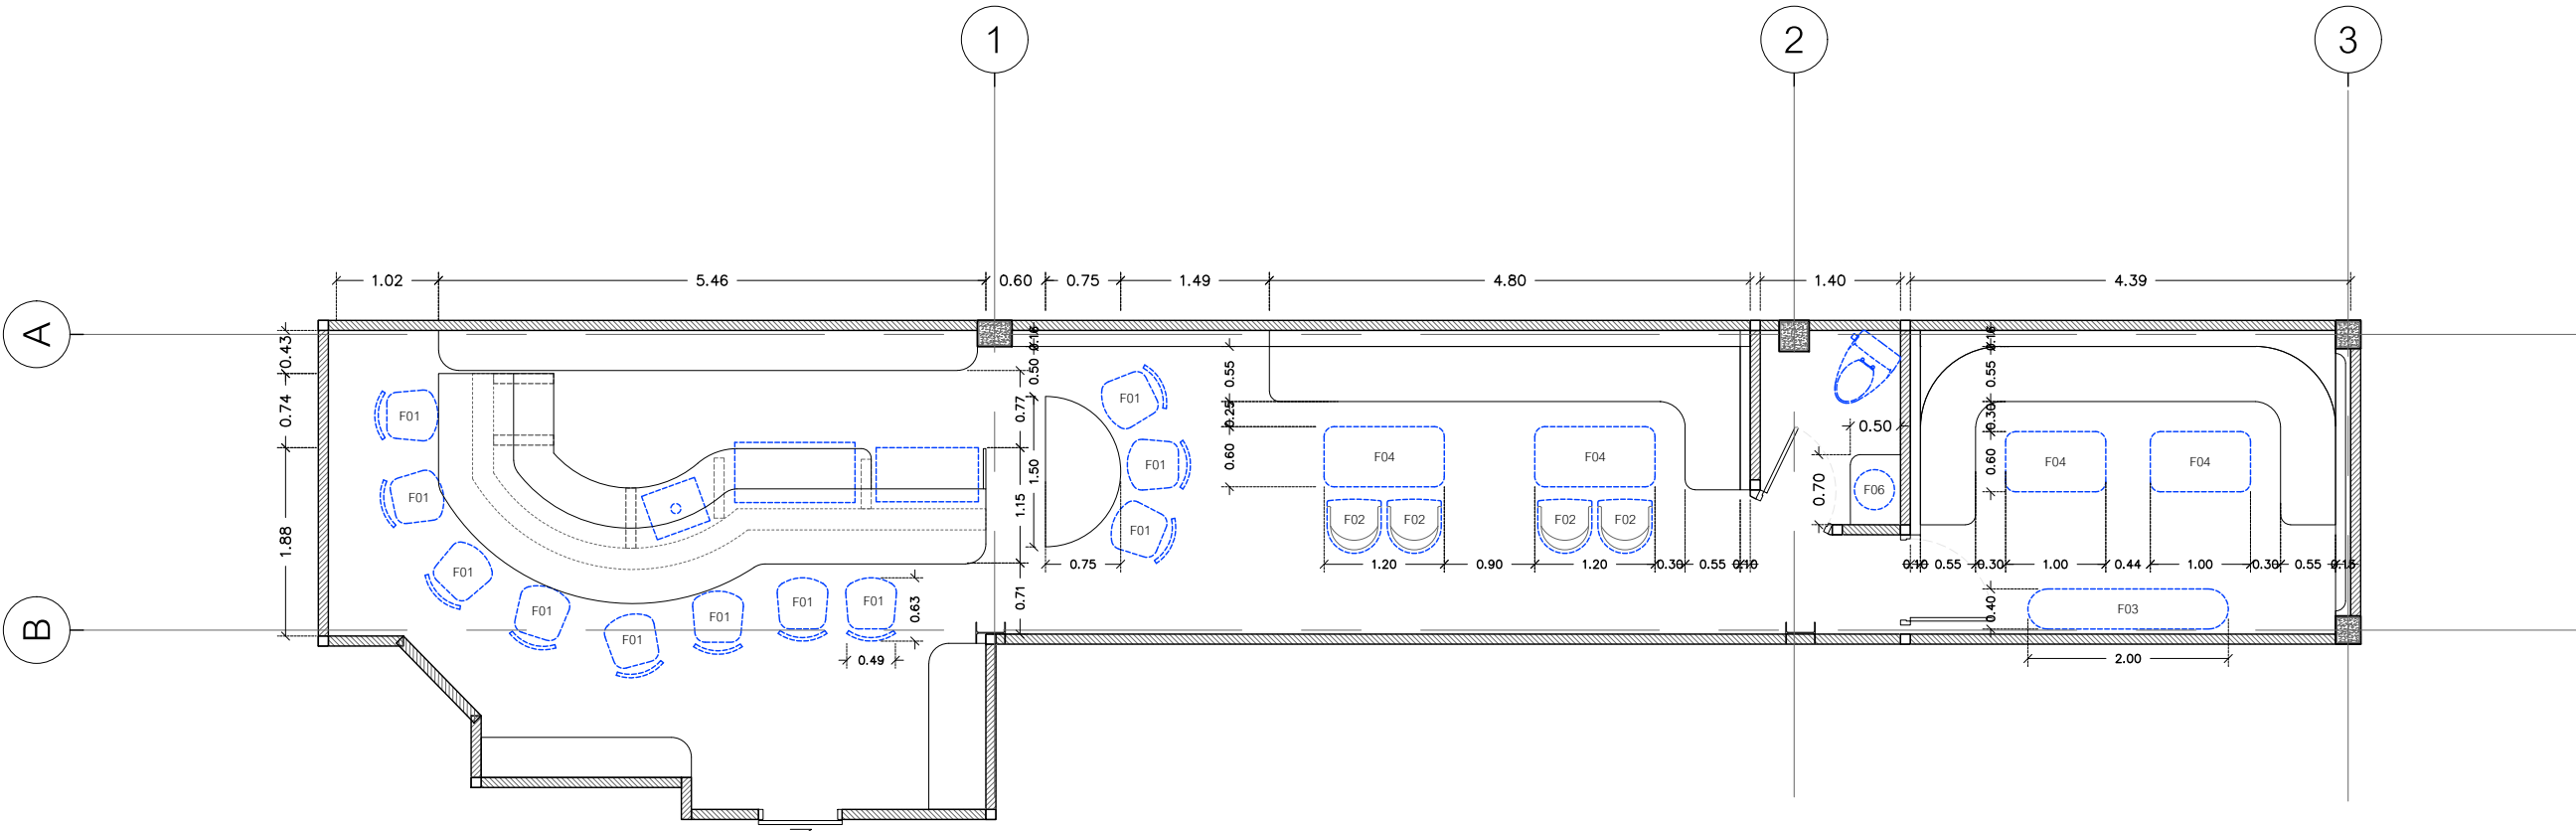

FURNITURE LAYOUT

SCALE 1 : 75



PROJECT TITLE

OWNER

ARCHITECTS

STRUCTURAL ENGINEERS

INTERIOR DESIGNER

DRAWN BY

DRAWING TITLE

SCALE 1:75

NOTE :

USE WRITTEN DIMENSION ONLY
ใช้เขียนตัวเลขที่กำหนดไว้เท่านั้น
ห้ามวัดจากแบบ
วัดพื้นที่ทุกตารางก่อนคำนวณ

NO	DATE	DESCRIPTION

DATE / / 2568

DRAWING No. PAGE TOTAL.

A-

00



PROJECT TITLE

OWNER

ARCHITECTS

STRUCTURAL ENGINEERS

INTERIOR DESIGNER

DRAWN BY

DRAWING TITLE

SCALE 1:75

NOTE :

USE WRITTEN DIMENSION ONLY
ใช้เขียนตัวเลขที่กำหนดไว้เท่านั้น
ห้ามวัดจากแบบ
วัดพื้นที่ทุกตารางก่อนดำเนินการ

NO	DATE	DESCRIPTION

DATE / / 2568

DRAWING No. PAGE TOTAL.


A-

00

BUILT-IN FURNITURE		
CODE	SYMBOL	DESCRIPTION
WC		Product: One-piece toilet Brand: BATH&BATH Model: SARO BT-4057 Flush system: Dual flush 3/4.5 liters Type: Floor-mounted, one-piece ceramic toilet
WB		Product: BJÖRKAN Washbasin with pop-up waste and mixer tap Color: White Size: 54×40 cm Included: Washbasin, trap, and single-lever mixer tap Brand: IKEA
MB		Product: Mirror Brand: IKEA Model: LINDBYN Color: Black Size: 50 cm (diameter) Type: Round wall-mounted mirror with black aluminum frame

BUILT-IN FURNITURE		
CODE	SYMBOL	DESCRIPTION
BF01		W 5380 D 2610 H 1100 Couter Bar
BF02		W 3800 D 400 H2660 Shelf
BF03		W 2220 D 1110 H 1100 Couter Bar
BF04		W 4700 D 1430 H 850 L-shaped sofa with backrest
BF05		W 7370 D 160 H 850 Sofa booth structure
BF06		W 4240 D 2040 H 850 U-shaped sofa with backrest
BF07		W 2670 D 150 H 2660 Sofa booth structure
BF08		W 1660 D 500 H 2660 Cabinet
BF09		W 2100 D 400 H 1100 Table
		The blue dashed line indicates items provide by the owner

BUILT-IN FURNITURE		
CODE	SYMBOL	DESCRIPTION
SINK		W 600 D 400 H 880 Couter Bar
FREEZER		W 1020 D 5400 H 800 Shelf
REFRIGERATOR		W 1200 D 600 H 800 Couter Bar

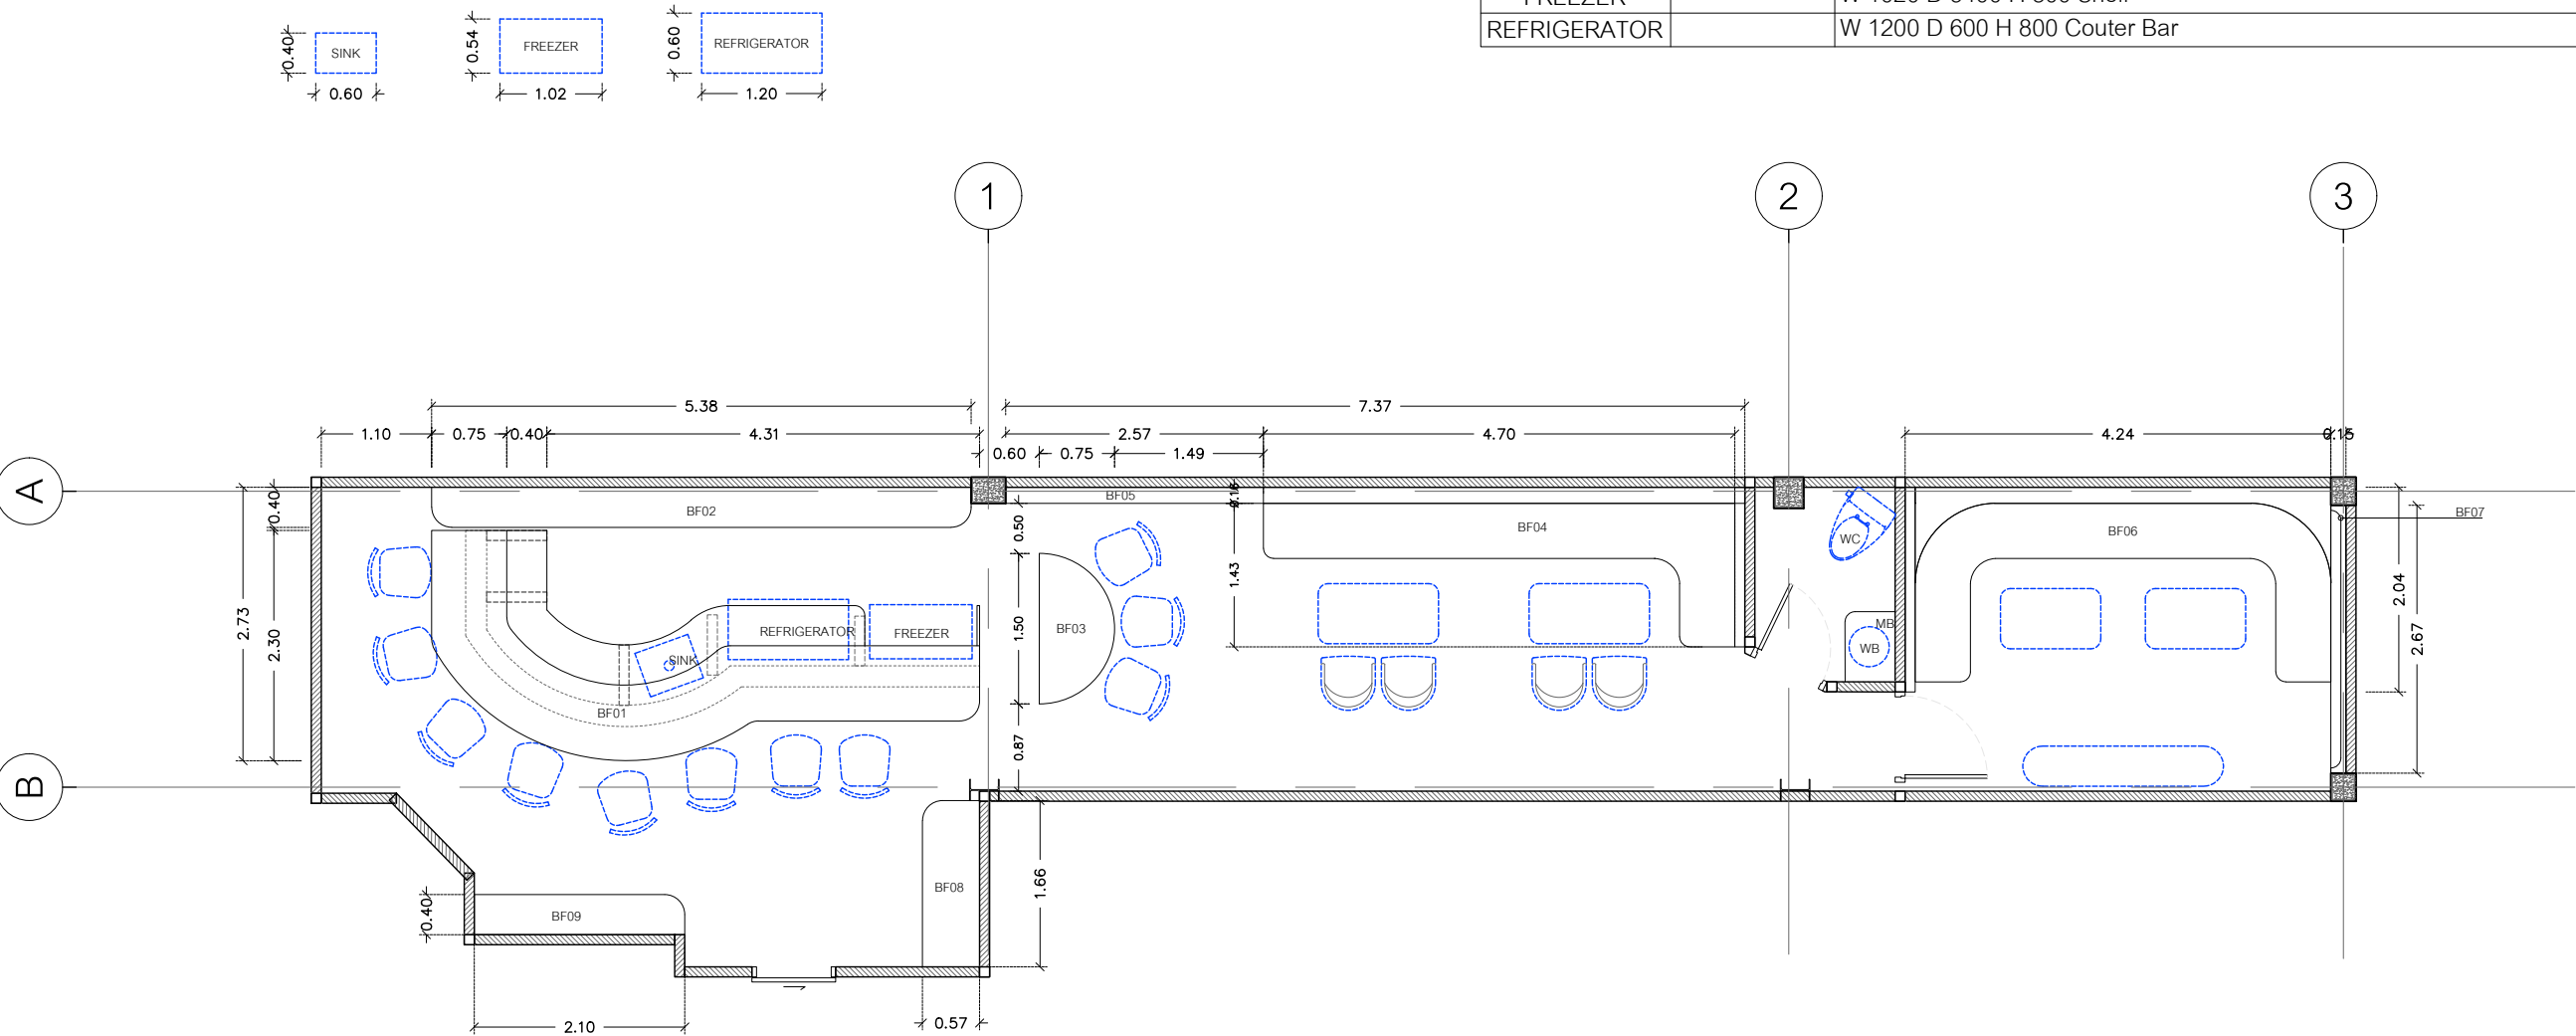

BUILT-IN FURNITURE LAYOUT

SCALE 1 : 75



PROJECT TITLE

OWNER

ARCHITECTS

STRUCTURAL ENGINEERS

INTERIOR DESIGNER

DRAWN BY

DRAWING TITLE

SCALE 1:75

NOTE :

USE WRITTEN DIMENSION ONLY
ใช้เขียนตัวเลขที่กำหนดไว้เท่านั้น
ห้ามวัดจากแบบ
วัดพื้นที่ทุกห้องก่อนคำนวณ

NO	DATE	DESCRIPTION

DATE / / 2568


DRAWING No. PAGE TOTAL.

A-

00

FLOOR FINISHES

CODE	SYMBOL	DESCRIPTION
FL1	1	SPC FLOORING NO. 4028 1220x183x4mm

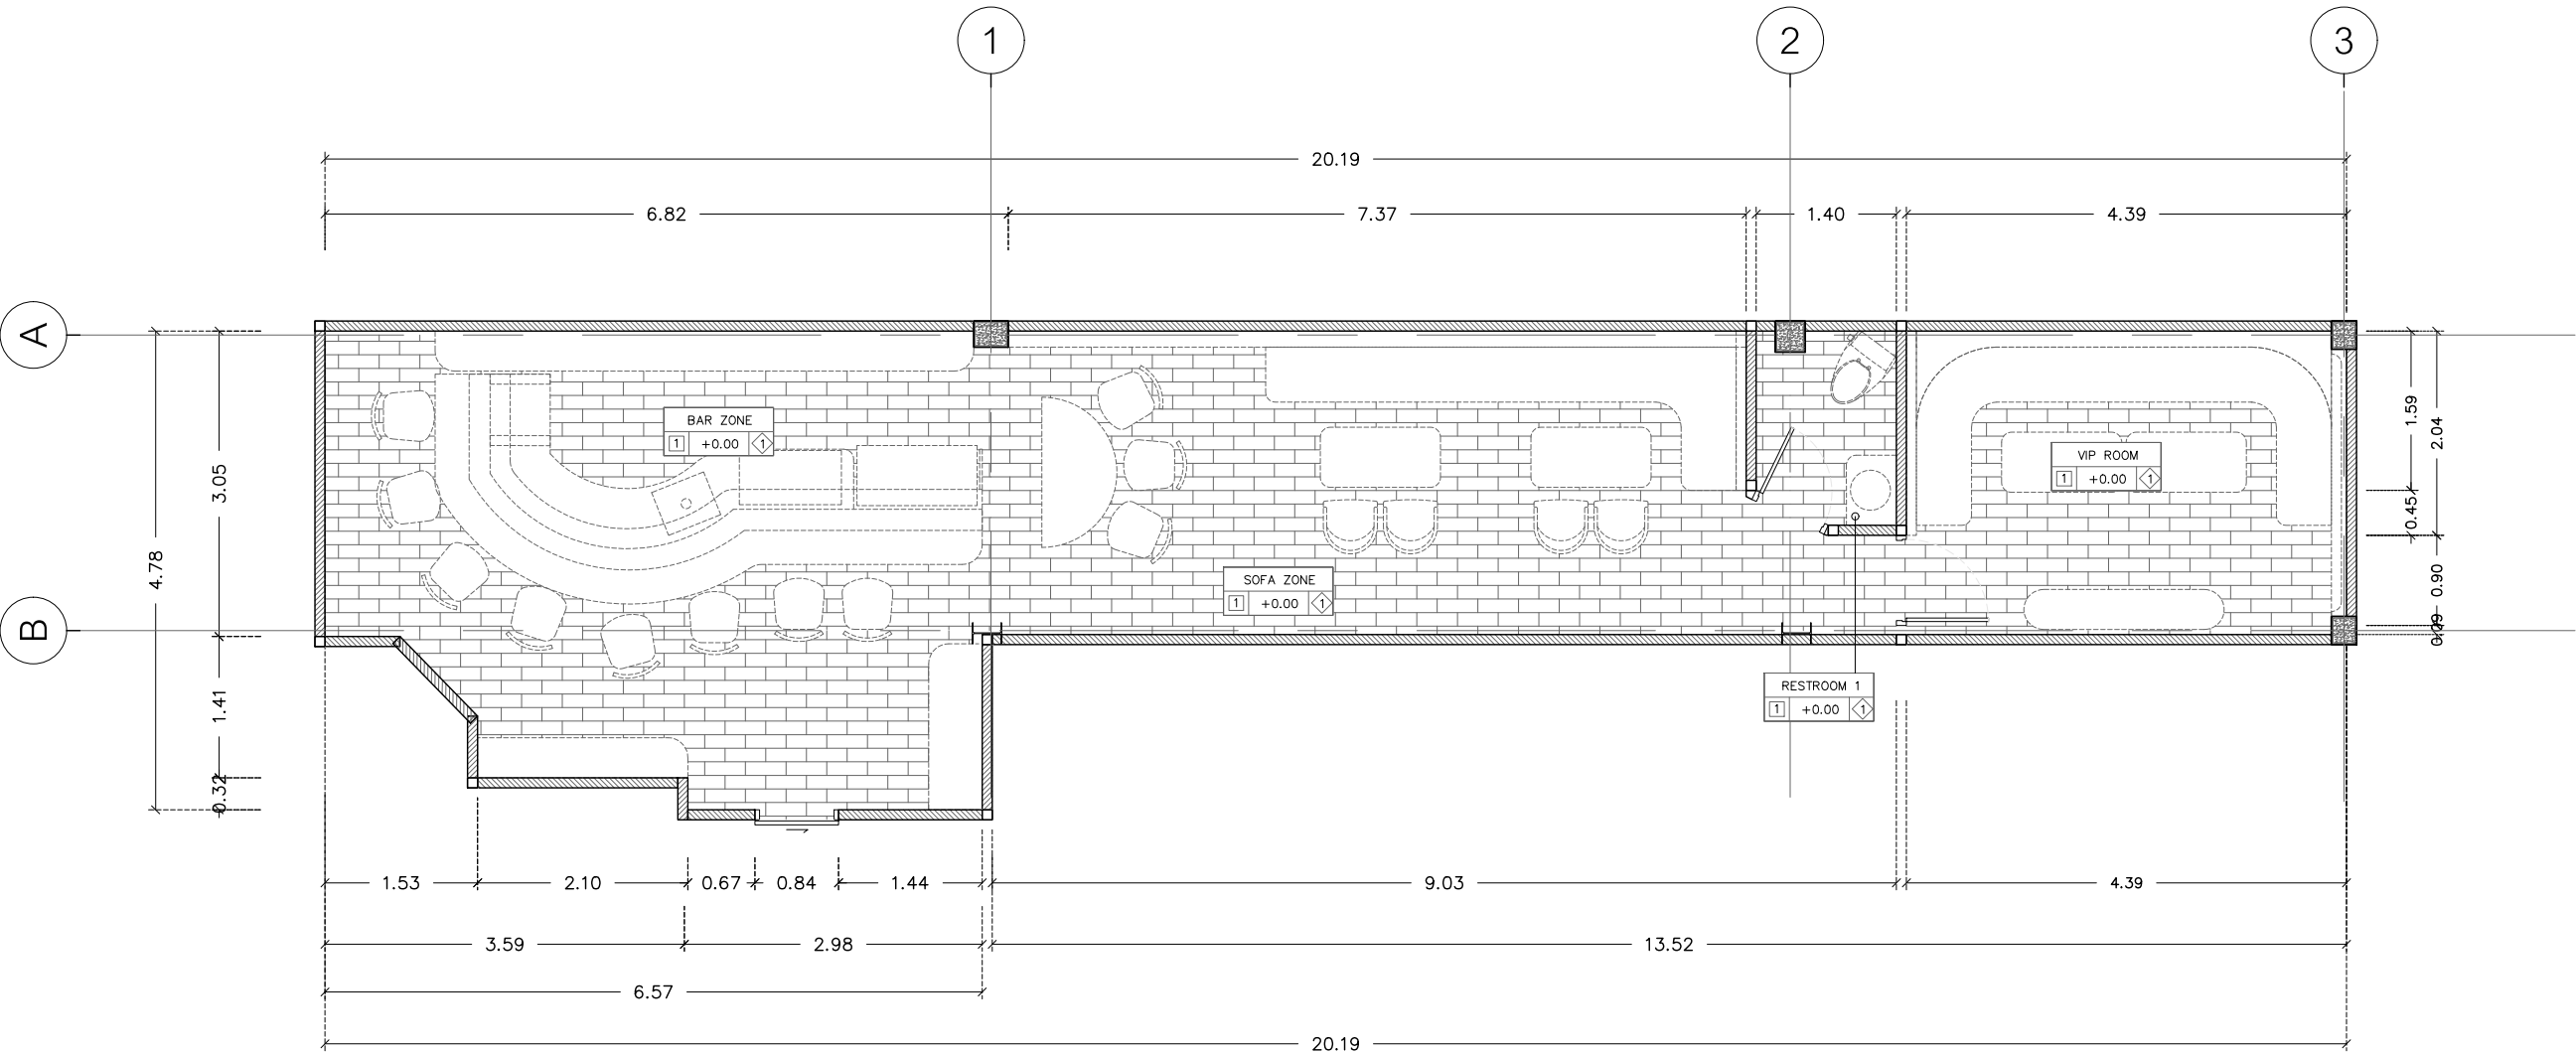

FLOOR FINISHES PLAN

SCALE 1 : 75



PROJECT TITLE

OWNER

ARCHITECTS

STRUCTURAL ENGINEERS

INTERIOR DESIGNER

DRAWN BY

DRAWING TITLE

SCALE 1:75

NOTE :

USE WRITTEN DIMENSION ONLY
ใช้เขียนตัวเลขที่กำหนดไว้เท่านั้น
ห้ามวัดจากแบบ
วัดพื้นที่ทุกห้องก่อนดำเนินการ

NO	DATE	DESCRIPTION

DATE / / 2568


DRAWING No. PAGE TOTAL.

A-

00

CEILING FINISHES

CODE	SYMBOL	DESCRIPTION
FL1	◊	Repair existing ceiling to operational condition.

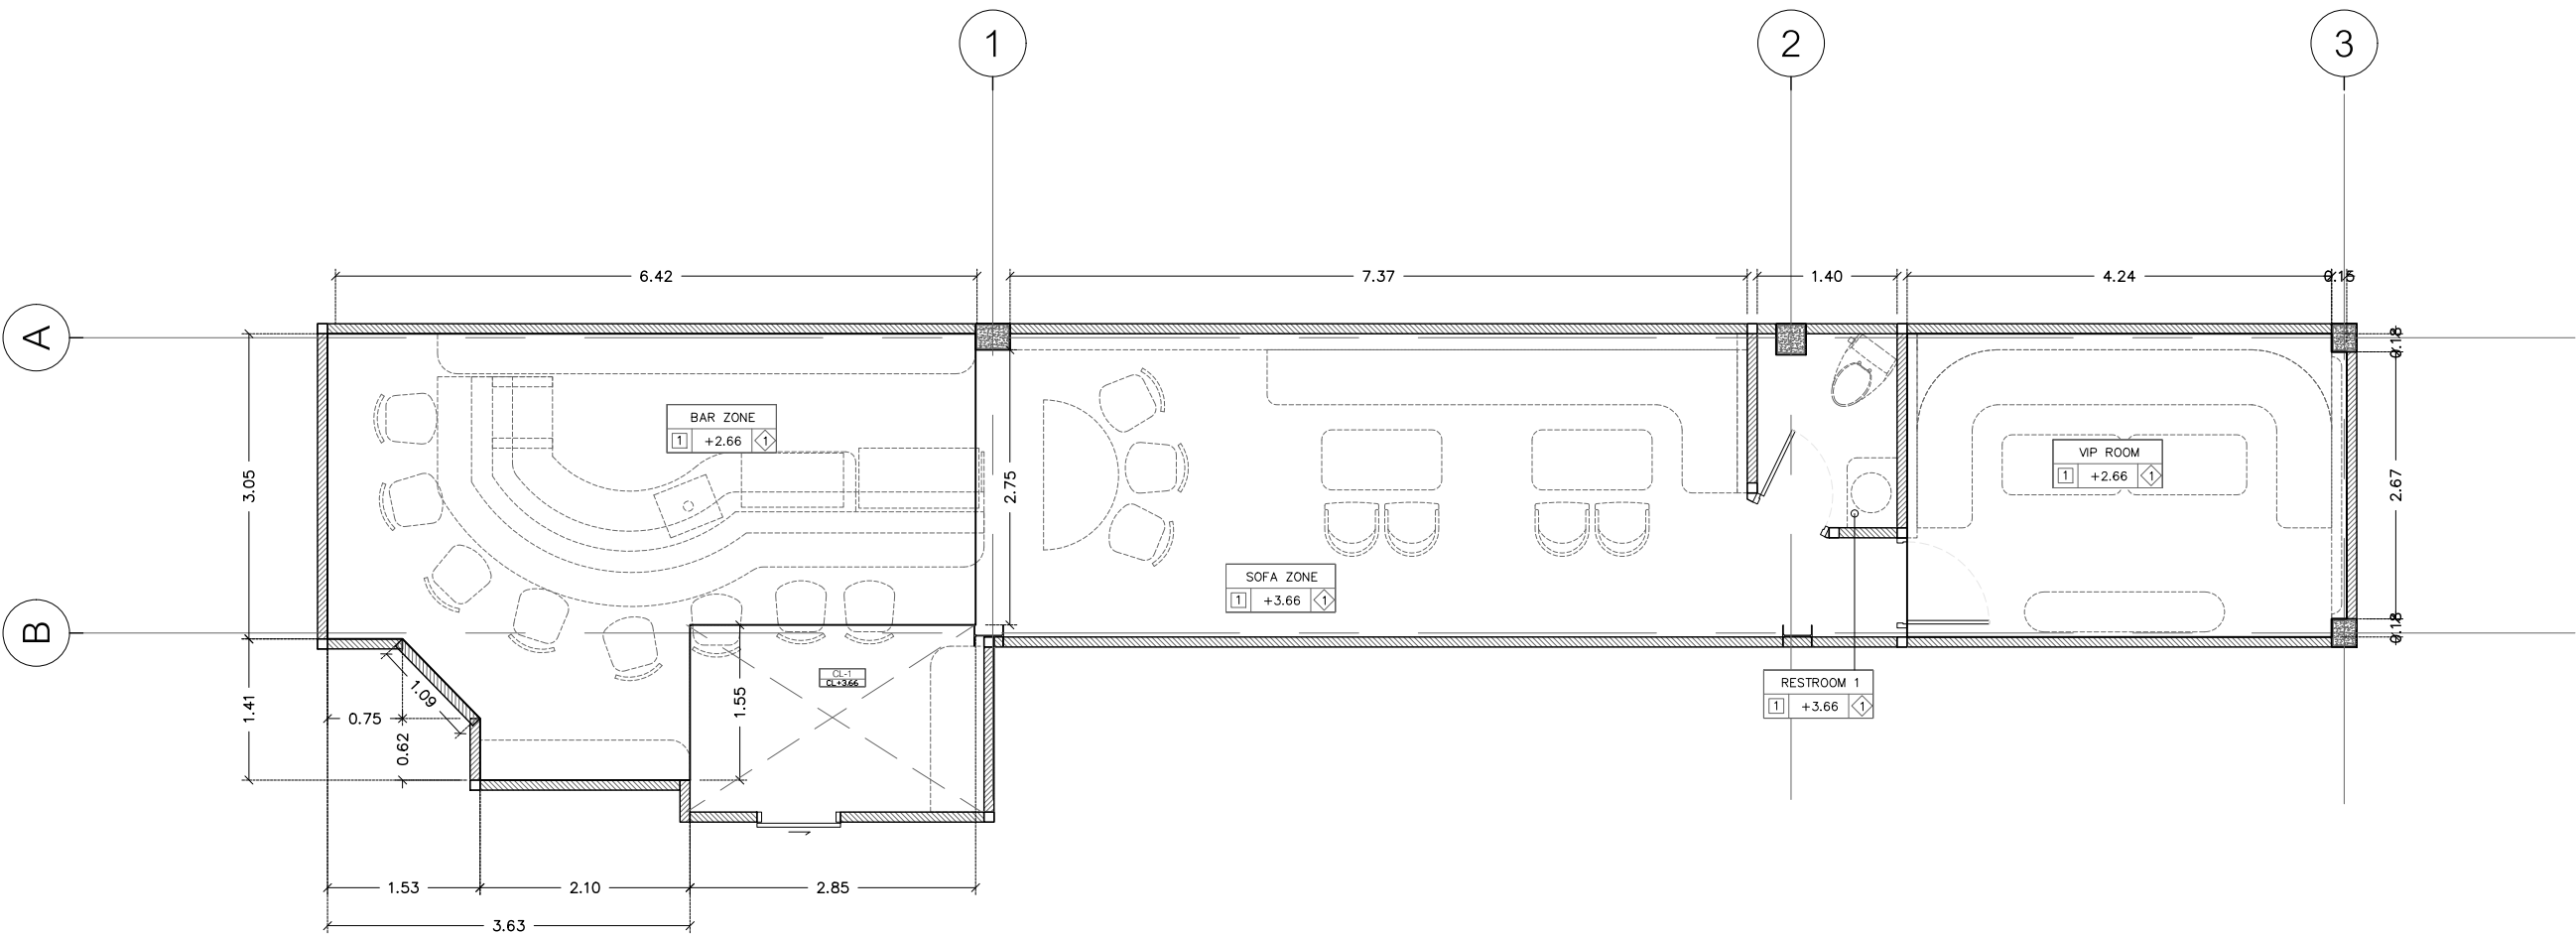


CEILING PLAN

SCALE 1 : 75

DOOR DESCRIPTION		
CODE	SYMBOL	DESCRIPTION
D1	Ⓐ	Single sliding door 0.80x200 m frame not included.
D2	Ⓑ	Provide single-leaf door, 0.80x2.00 m frame not included.
D3	Ⓒ	Provide single-leaf door, 0.70x2.00 m frame not included.

WALL FINISHES		
CODE	SYMBOL	DESCRIPTION
WF1	Ⓐ	Repair existing wall and paint black
WF2	Ⓑ	Repair existing wall and paint red
WF3	Ⓒ	Construct lightweight concrete block wall, smooth render and paint red
WF4	Ⓓ	Construct lightweight concrete block wall, smooth render and paint black
WF5	Ⓔ	Wall panel with 8 mm thick HMR board, finished with black wood grain laminate, code to be specified later.
WF6	Ⓕ	Wall tiled up to 1.2 meters height

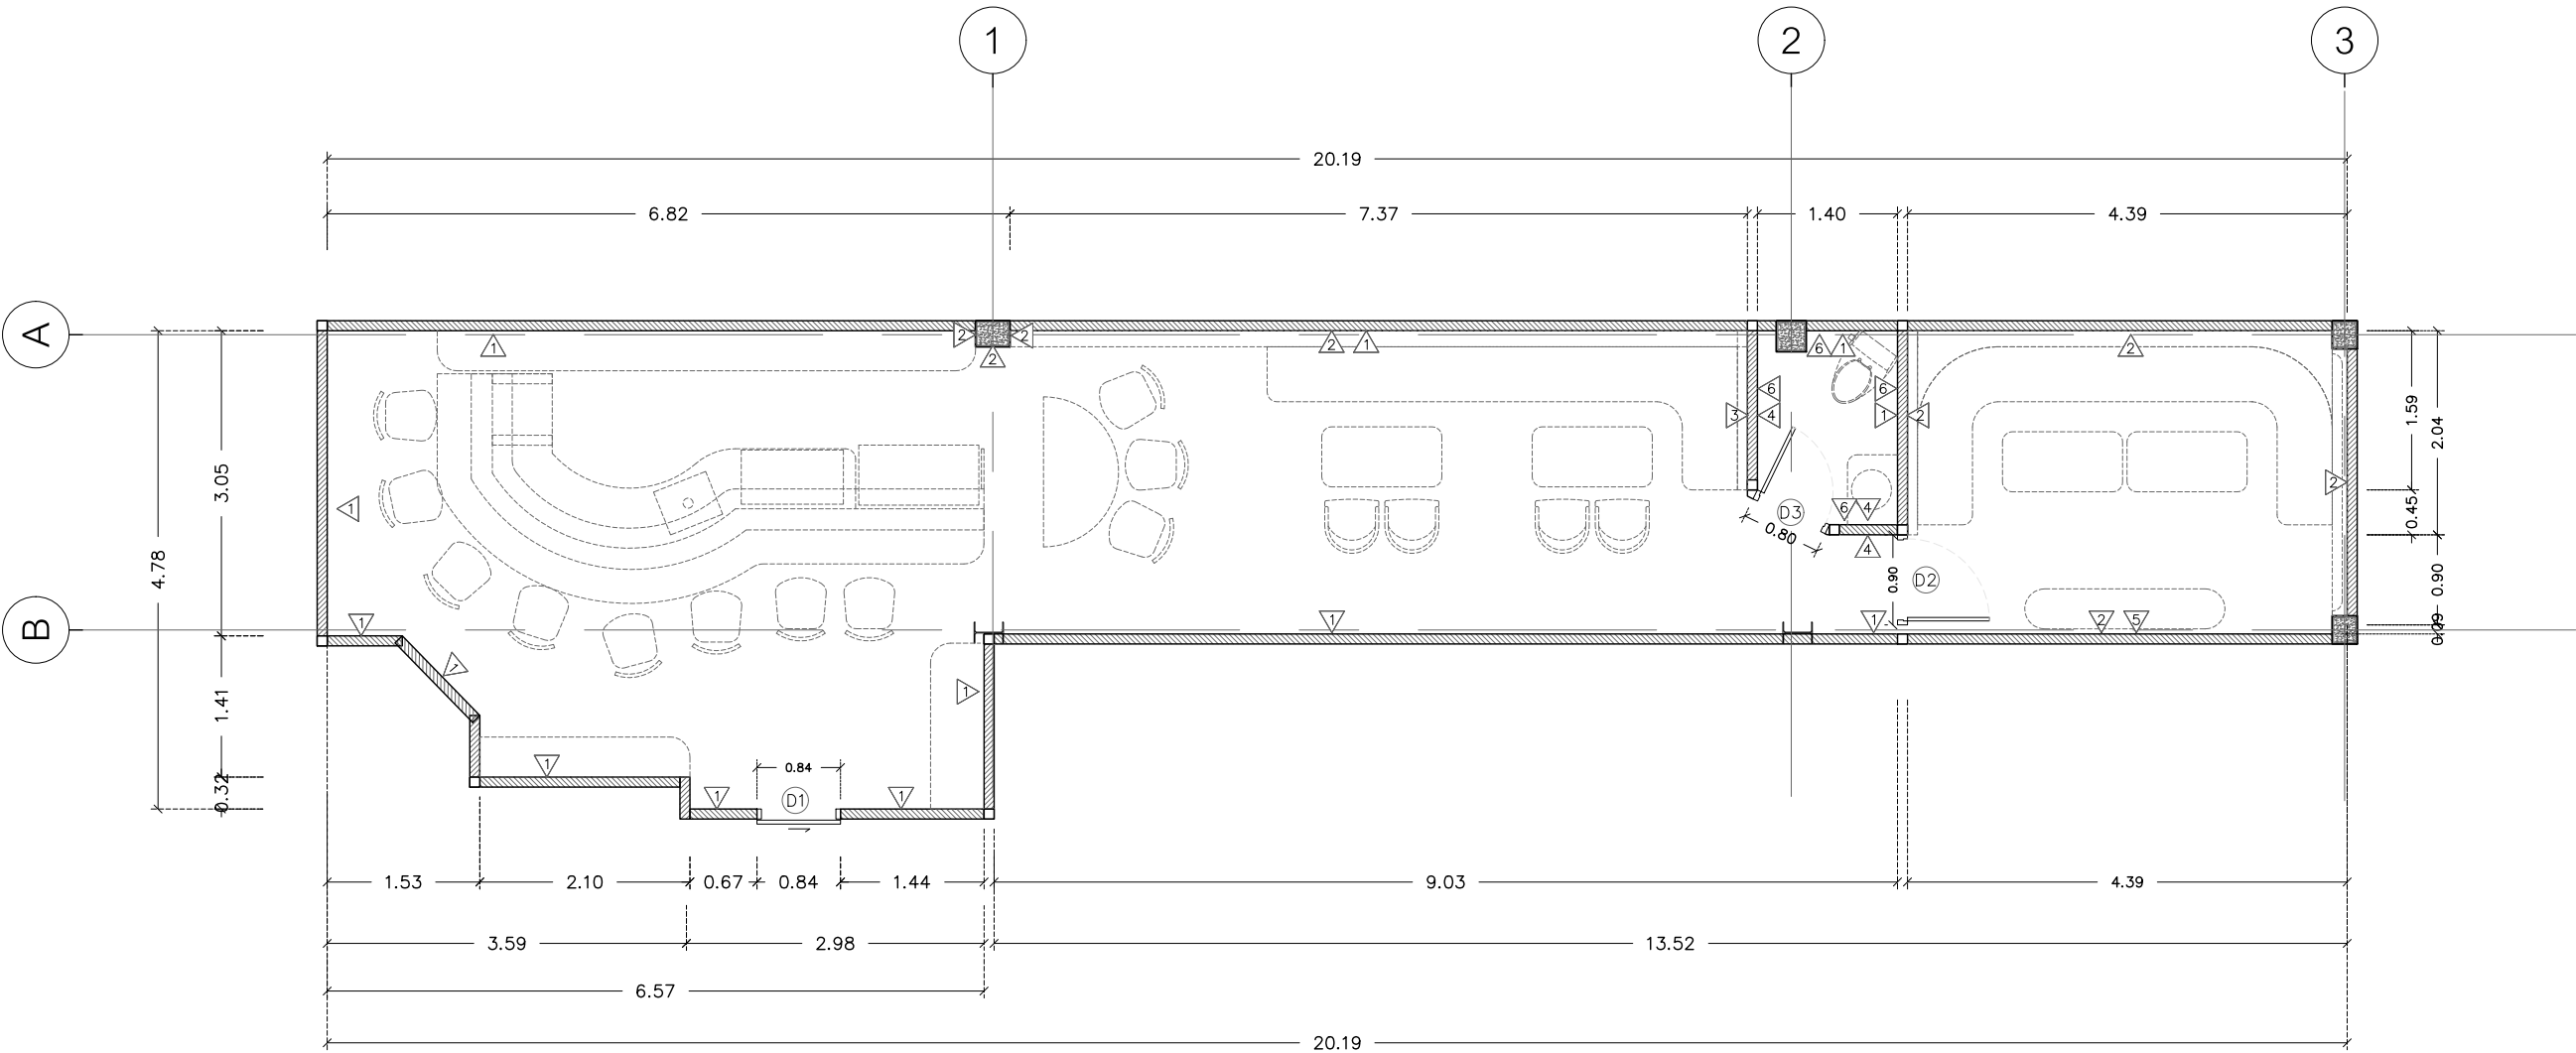

WALL FINISHES/DOOR PLAN

SCALE 1 : 75



PROJECT TITLE

OWNER

ARCHITECTS

STRUCTURAL ENGINEERS

INTERIOR DESIGNER

DRAWN BY

DRAWING TITLE

SCALE 1:75


NOTE :

USE WRITTEN DIMENSION ONLY
ใช้คำตัวเลขที่กำหนดไว้เท่านั้น
ห้ามวัดจากแบบ
วัดพื้นที่ทุกสิ่งก่อนดำเนินการ


NO	DATE	DESCRIPTION

DATE / / 2568

DRAWING No.	PAGE TOTAL
A-	00

 LIGHTING CIRCUIT		
CODE	SYMBOL	DESCRIPTION
LT01		RECESSED DOWNLIGHT, DIMENSIONS 5X5-10X10 CM (WXL).
LT02		PROVIDE AND INSTALL PENDANT LIGHT, DIMENSIONS 20X20 CM (WXL).
LT03		TACK LIGHT 2M LED DIMMABLE GU10 LUMINAR 7W WARMWHITE BEAM 24D TRACK LIGHT FIXTURE, CYLINDRICAL SHAPE, GU10 BASE, WITH HONEYCOMB LOUVER, BLACK FINISH
LT04		TACK LIGHT 3M LED DIMMABLE GU10 LUMINAR 7W WARMWHITE BEAM 24D TRACK LIGHT FIXTURE, CYLINDRICAL SHAPE, GU10 BASE, WITH HONEYCOMB LOUVER, BLACK FINISH
LT05		ORIGINAL HANGING LIGHT FIXTURE
LT06		PROVIDE AND INSTALL WARM WHITE LED STRIP LIGHT (2700K-3000K)
LT07		PROVIDE AND INSTALL PENDANT LIGHT, DIMENSIONS 20X10 CM (WXL) LED DIMMABLE GU10 LUMINAR 7W WARMWHITE BEAM 24D
LT08		PROVIDE LED LIGHTBOX SIGN FOR SHOPFRONT, INCLUDING STRUCTURE, WIRING, AND INSTALLATION.

LIGHTING CIRCUIT		
CODE	SYMBOL	DESCRIPTION
		1-Way Switch Brand/Model: PANASONIC WEGN5531H Type: 1-gang, 1-way switch Color: Grey
		Dimmer Switch Brand/Model: PANASONIC WEG57813H Type: 300W dimmer switch Color: Grey
		COMPUTER
		Provide double grounded socket outlet with safety shutter and cover plate
		CIRCUIT BREAKER BOX
		WIFI
		MAIN BOARD

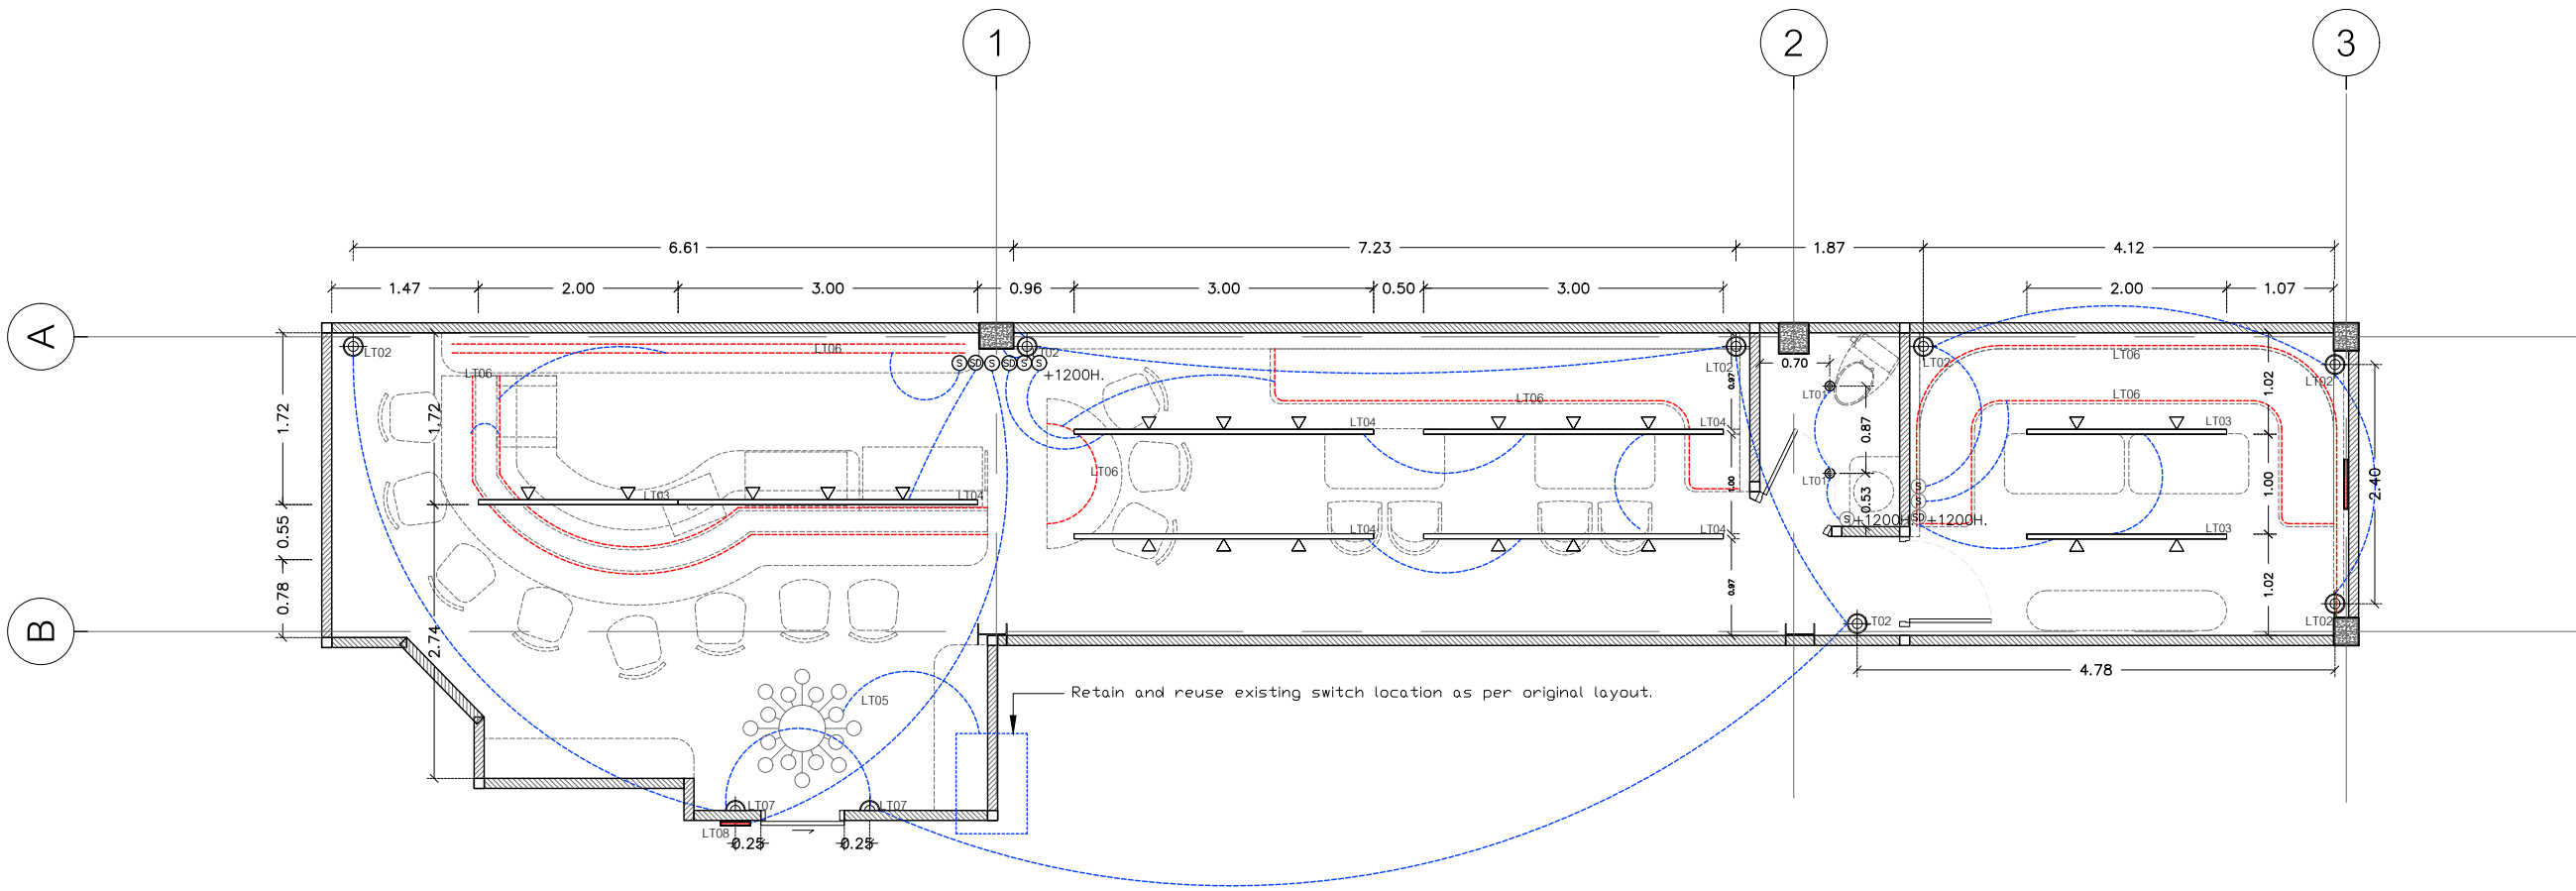

LIGHTING CIRCUIT PLAN

SCALE 1 : 75



PROJECT TITLE

OWNER

ARCHITECTS

STRUCTURAL ENGINEERS

INTERIOR DESIGNER

DRAWN BY

DRAWING TITLE

SCALE 1:75

NOTE :

USE WRITTEN DIMENSION ONLY
ใช้คำตัวเลขที่กำหนดไว้เท่านั้น
ห้ามวัดจากแบบ
วัดพื้นที่ทุกครั้งที่ก่อนดำเนินการ

NO	DATE	DESCRIPTION


DATE / / 2568

DRAWING No. PAGE TOTAL.

A-

00

LIGHTING CIRCUIT		
CODE	SYMBOL	DESCRIPTION
	(S)	SWITCH
	(Sw)	WATERPROOF SWITCH
	(L)	COMPUTER
	(⊖)	Provide double grounded socket outlet with safety shutter and cover plate
	(CB)	CIRCUIT BREAKER BOX
	(Wireless)	WIFI
	(Main Board)	MAIN BOARD
	(Conduit)	Install main electrical conduit and wiring for built-in furniture.
	(TV 40")	TV 40"

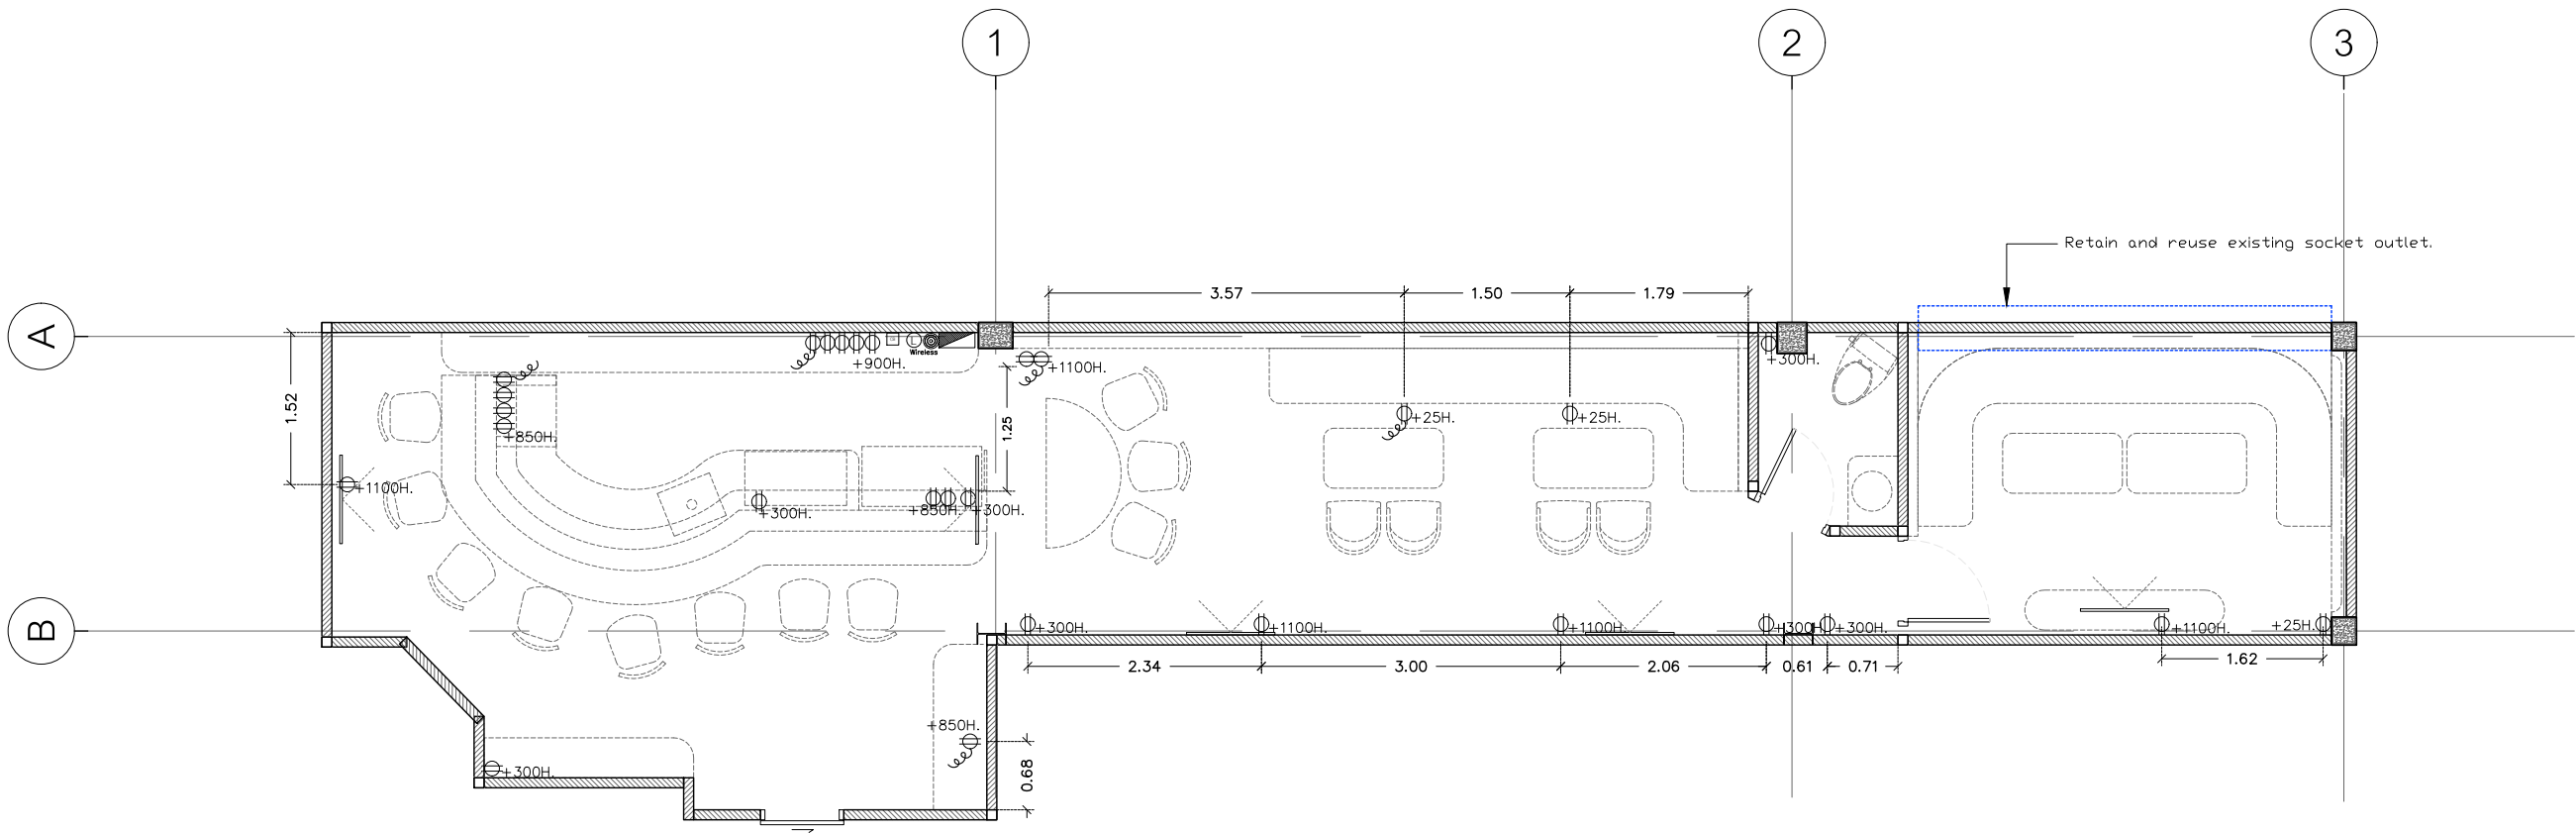

ELECTRICAL PLAN

SCALE 1 : 75



PROJECT TITLE

OWNER

ARCHITECTS

STRUCTURAL ENGINEERS

INTERIOR DESIGNER

DRAWN BY

DRAWING TITLE

SCALE 1:75

NOTE :

USE WRITTEN DIMENSION ONLY
ใช้เขียนตัวเลขที่กำหนดไว้เท่านั้น
ห้ามวัดจากแบบ
วัดพื้นที่ทุกตารางก่อนดำเนินการ

NO	DATE	DESCRIPTION

DATE / / 2568

DRAWING No. PAGE TOTAL.

A-

00

LIGHTING CIRCUIT		
CODE	SYMBOL	DESCRIPTION
		AIR CONDITION
		THERMOSTAT



PROJECT TITLE

OWNER

ARCHITECTS

STRUCTURAL ENGINEERS

INTERIOR DESIGNER

DRAWN BY

DRAWING TITLE

SCALE 1:75

NOTE :

USE WRITTEN DIMENSION ONLY
ใช้เขียนตัวเลขที่กำหนดไว้เท่านั้น
ห้ามวัดจากแบบ
วัดพื้นที่ทุกตารางก่อนดำเนินการ


NO	DATE	DESCRIPTION

DATE / / 2568

DRAWING No. PAGE TOTAL.

A-


00

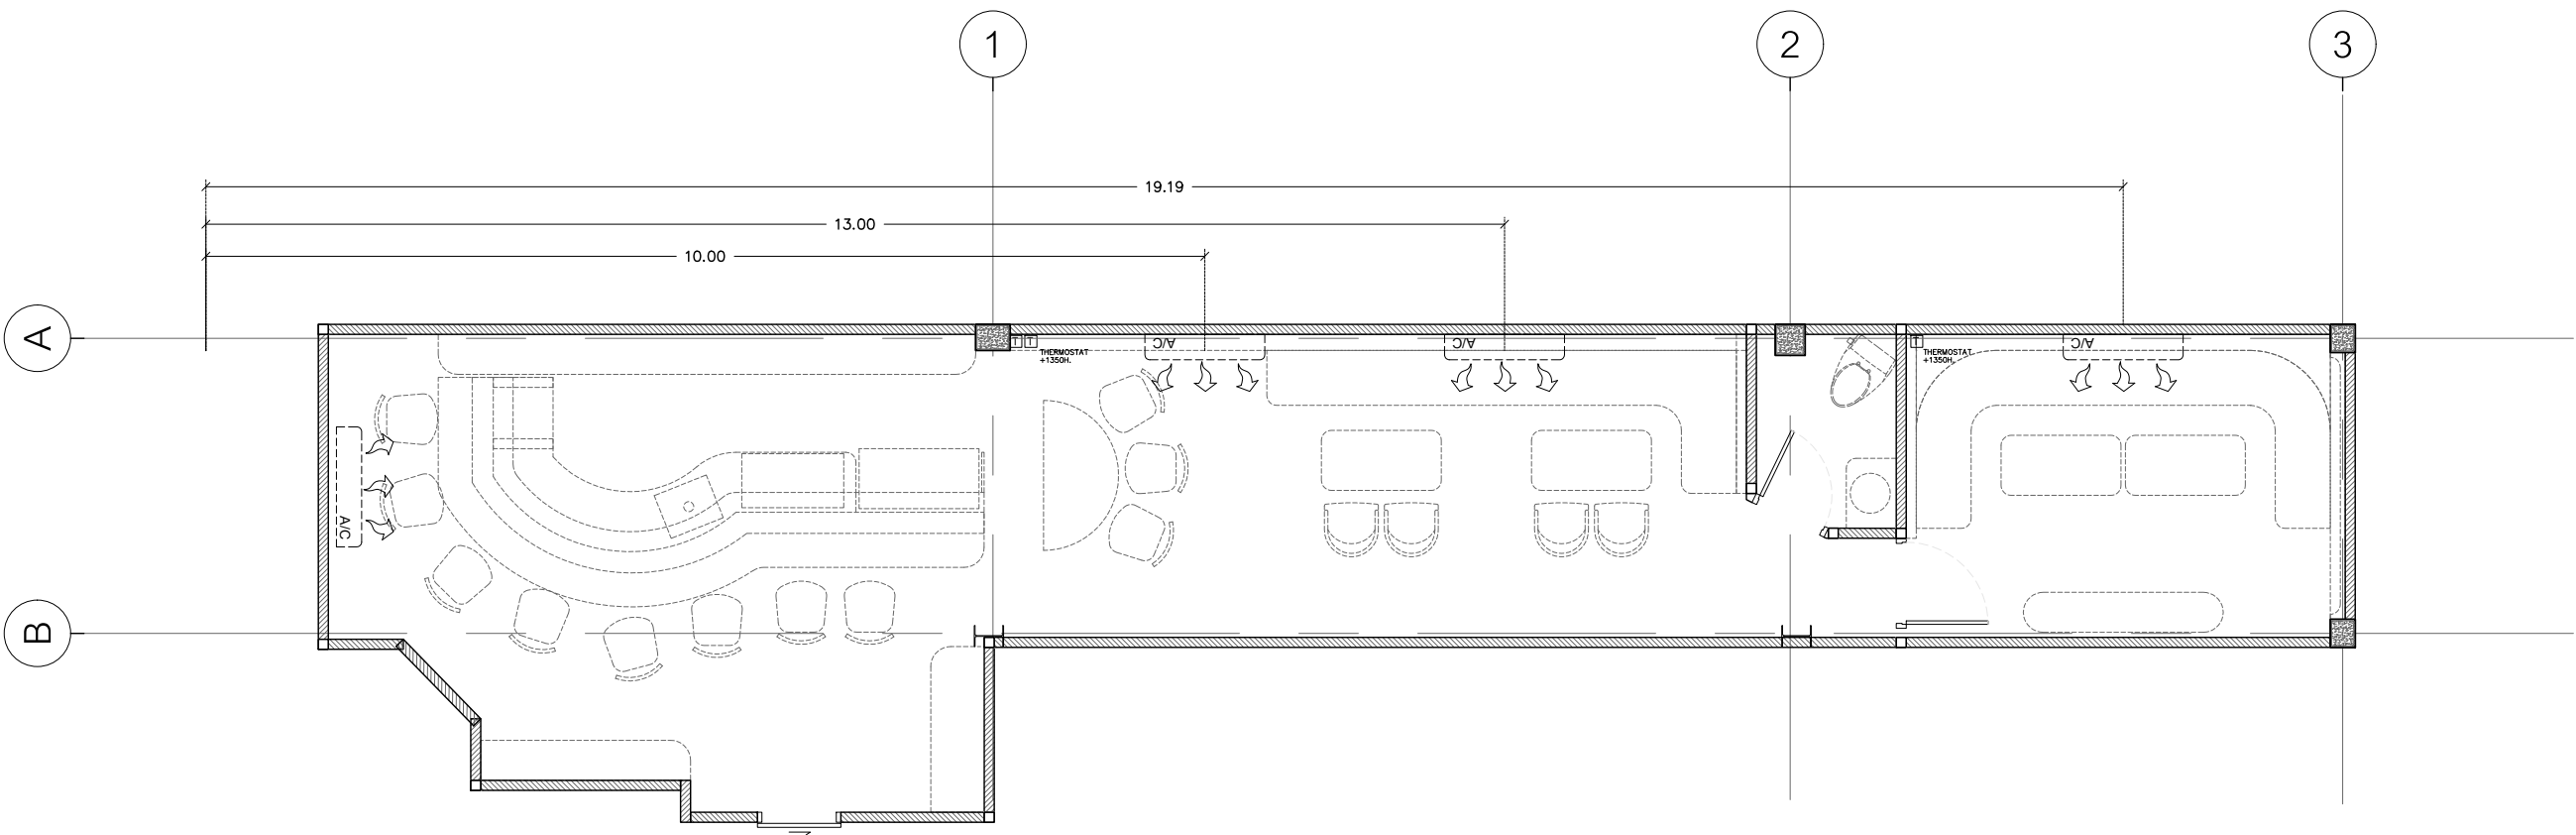

AIR CONDITIONING PLAN


SCALE 1 : 75

SANITARY SYSTEM		
CODE	SYMBOL	DESCRIPTION
		CW.PVC.Ø 1"
		W.PVC.Ø 2"
		S.PVC.Ø 4"
		Floor drain with trap and debris filter
		Water meter
		Gate valve
		Wastewater treatment tank
		Reinforced concrete manhole with cover

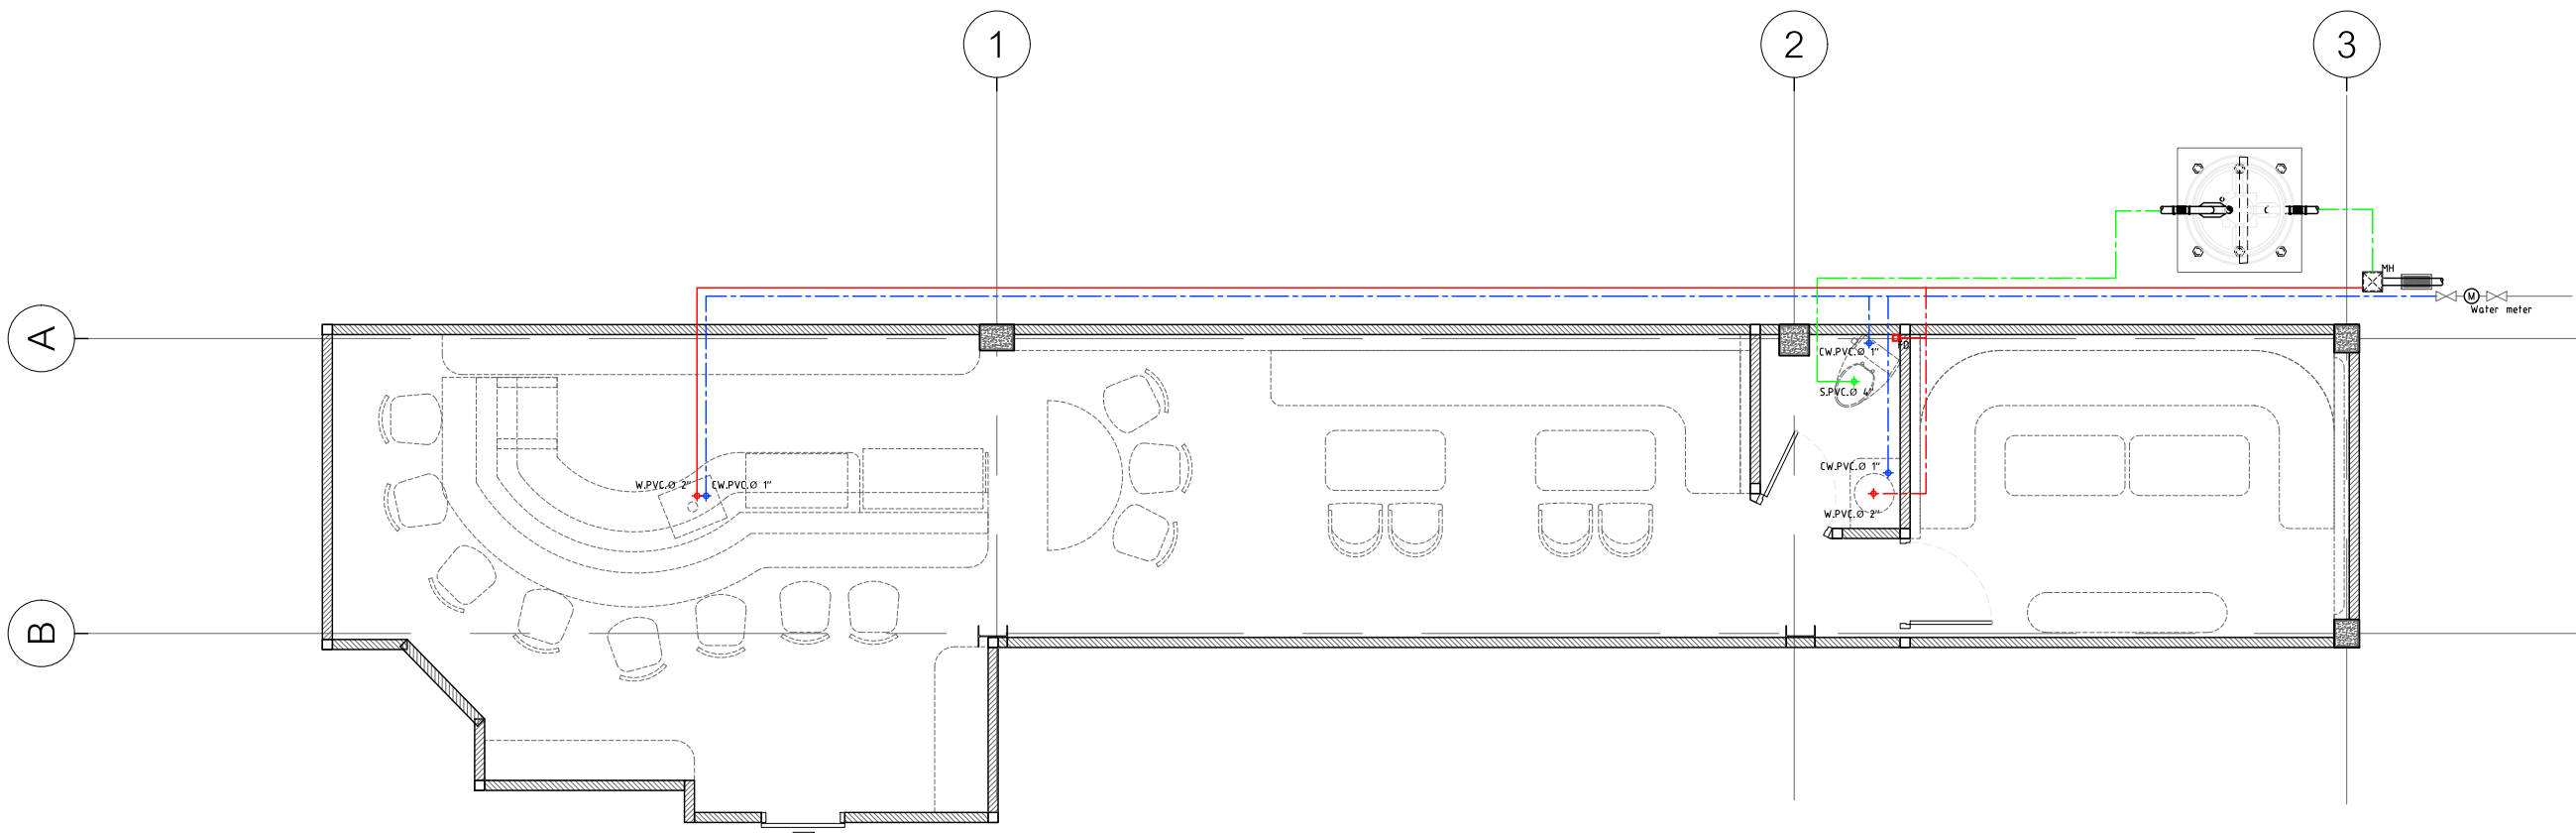

SANITARY SYSTEM PLAN

SCALE 1 : 75

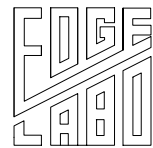

PROJECT TITLE

OWNER

ARCHITECTS

STRUCTURAL ENGINEERS

INTERIOR DESIGNER

DRAWN BY

DRAWING TITLE

SCALE 1:75

NOTE :

USE WRITTEN DIMENSION ONLY
ใช้เขียนตัวเลขที่กำหนดไว้เท่านั้น
ห้ามวัดจากแบบ
วัดพื้นที่ทุกครั้งที่ก่อนดำเนินการ


NO	DATE	DESCRIPTION
----	------	-------------

DATE / / 2568


DRAWING No.	PAGE TOTAL
-------------	------------

A-


00

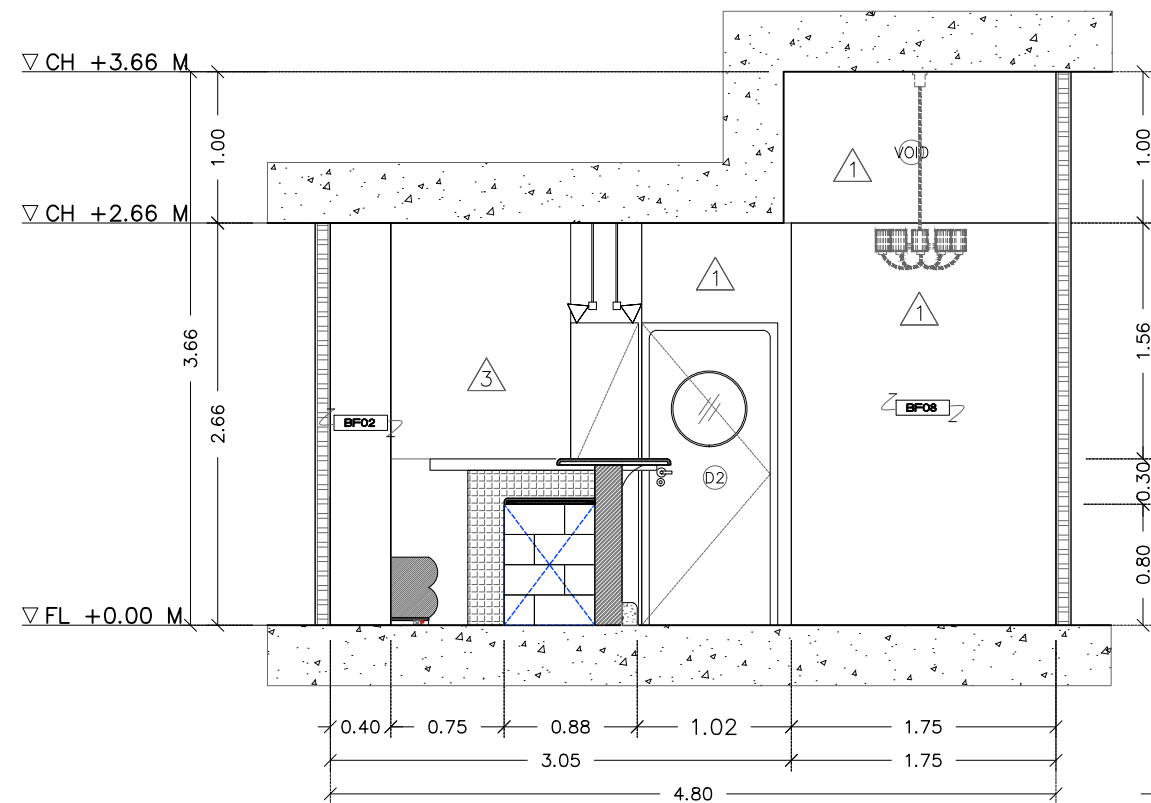


ELEVATION A
SCALE 1:50

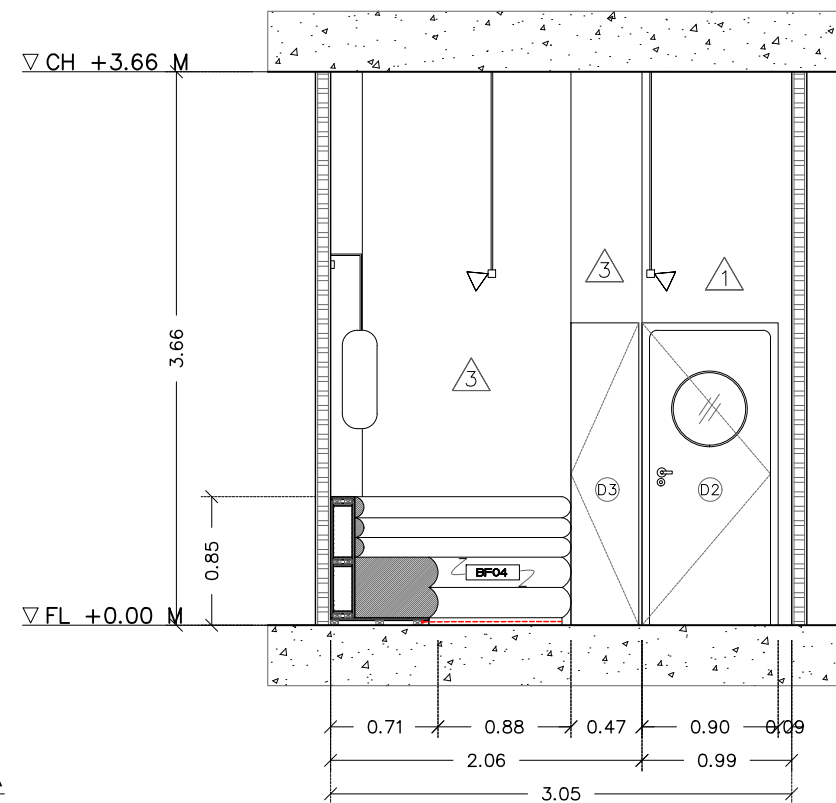

ELEVATION B
SCALE 1:50

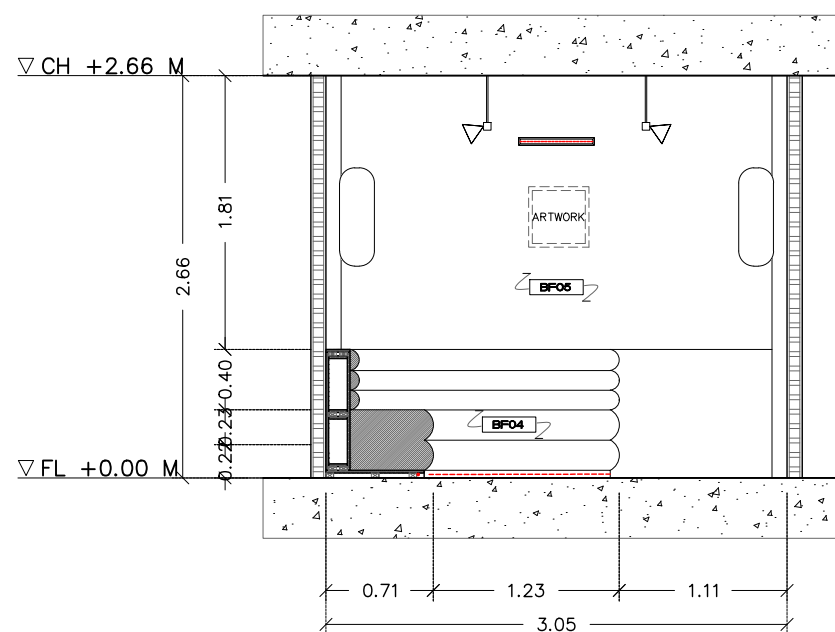

ELEVATION C
SCALE 1:50

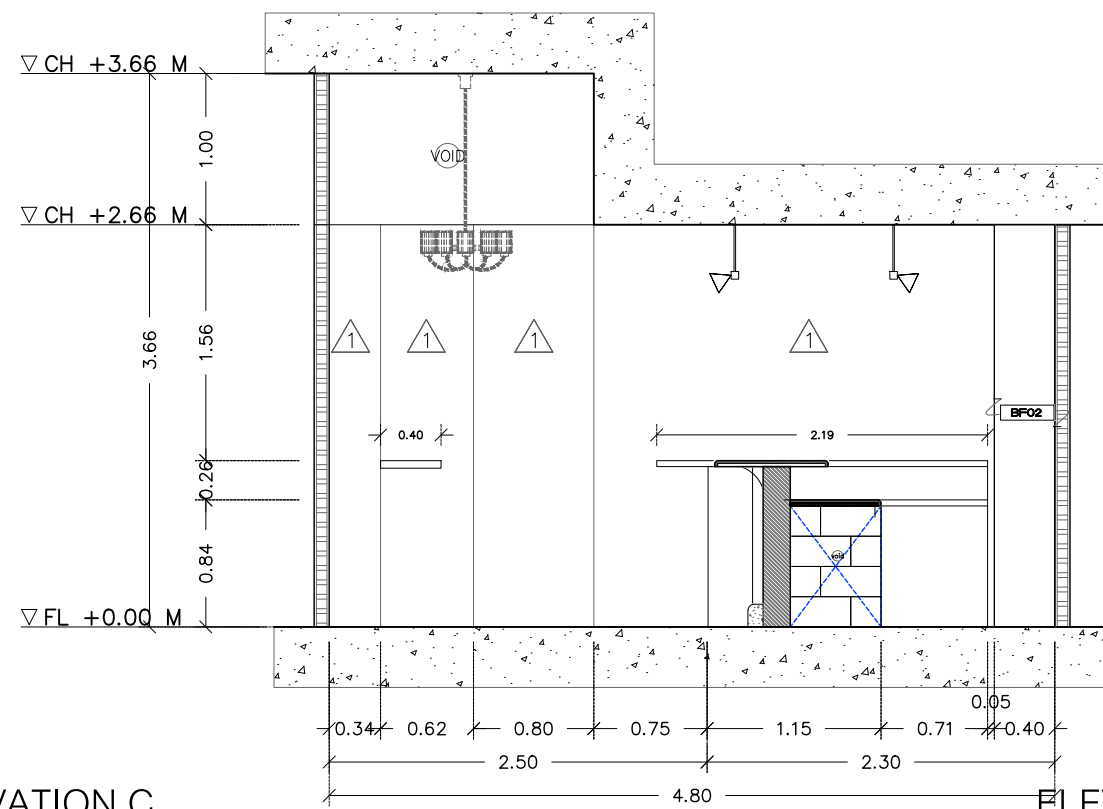

ELEVATION D
SCALE 1:50



PROJECT TITLE

OWNER

ARCHITECTS

STRUCTURAL ENGINEERS

INTERIOR DESIGNER

DRAWN BY

DRAWING TITLE

SCALE 1:75


NOTE :
USE WRITTEN DIMENSION ONLY
ใช้คำตัวเลขที่กำหนดไว้เท่านั้น
ห้ามวัดจากแบบ
วัดพื้นที่ทุกครั้งก่อนดำเนินการ

NO	DATE	DESCRIPTION


DATE / / 2568

DRAWING No. PAGE TOTAL.


A- 00

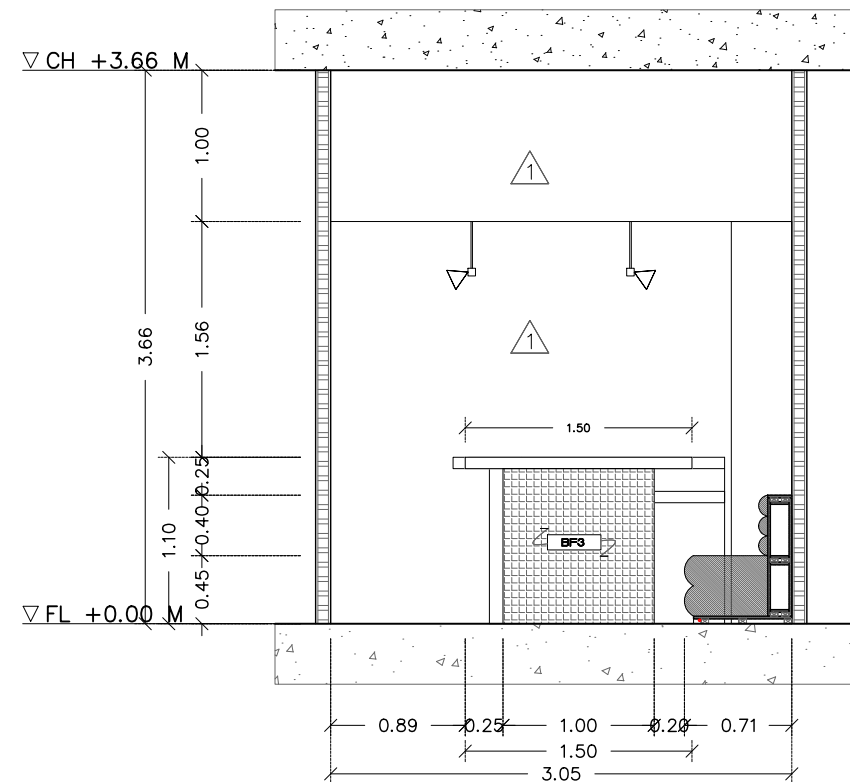

ELEVATION E
SCALE 1 : 50

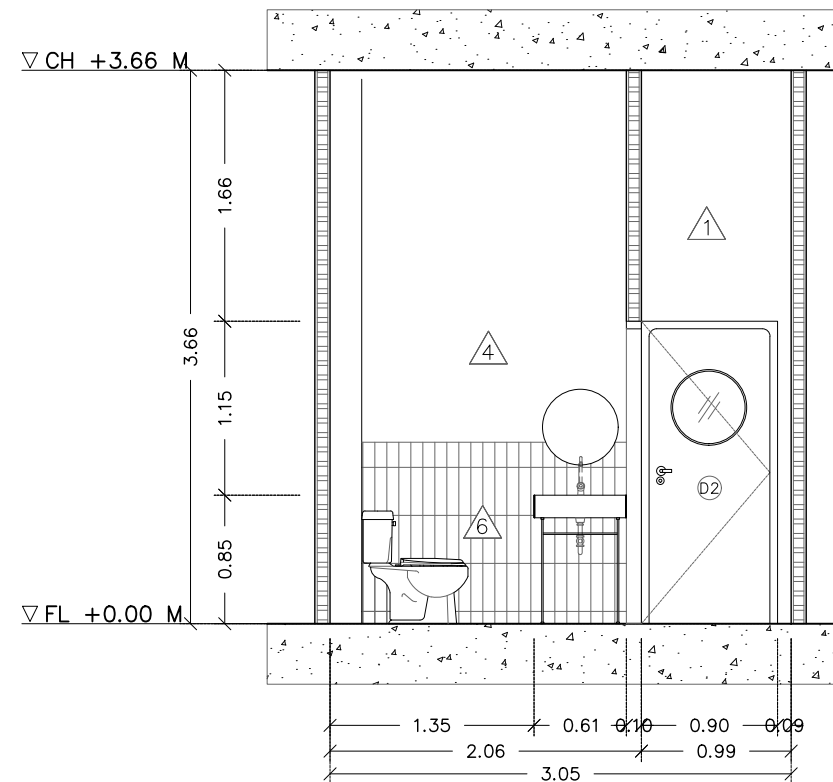

ELEVATION F
SCALE 1 : 50

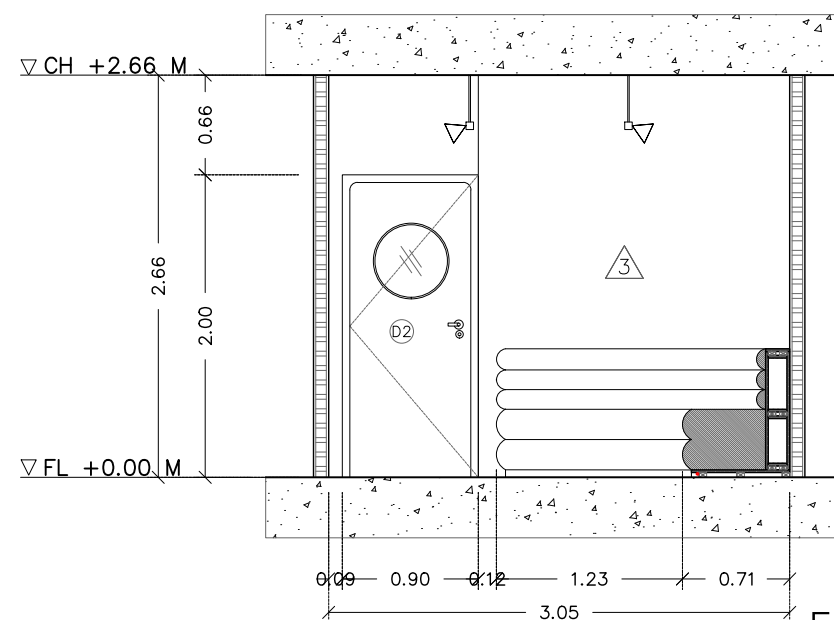

ELEVATION G
SCALE 1 : 50



PROJECT TITLE

OWNER

ARCHITECTS

STRUCTURAL ENGINEERS

INTERIOR DESIGNER

DRAWN BY

DRAWING TITLE

SCALE 1:75

NOTE :


USE WRITTEN DIMENSION ONLY
ใช้เขียนตัวเลขที่กำหนดไว้เท่านั้น
ห้ามวัดจากแบบ
วัดพื้นที่ทุกครั้งที่ก่อนดำเนินการ

NO	DATE	DESCRIPTION

DATE / / 2568

DRAWING No. PAGE TOTAL.

A- 00

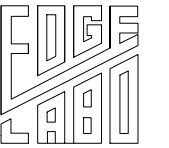

PROJECT TITLE

OWNER

ARCHITECTS

STRUCTURAL ENGINEERS

INTERIOR DESIGNER

DRAWN BY

DRAWING TITLE

SCALE 1:75

NOTE :

USE WRITTEN DIMENSION ONLY
ใช้เขียนค่าตัวเลขที่กำหนดไว้เท่านั้น
ห้ามวัดจากแบบ
วัดพื้นที่ทุกครั้งที่ก่อนดำเนินการ


NO	DATE	DESCRIPTION

DATE / / 2568

DRAWING No. PAGE TOTAL.


A-

00

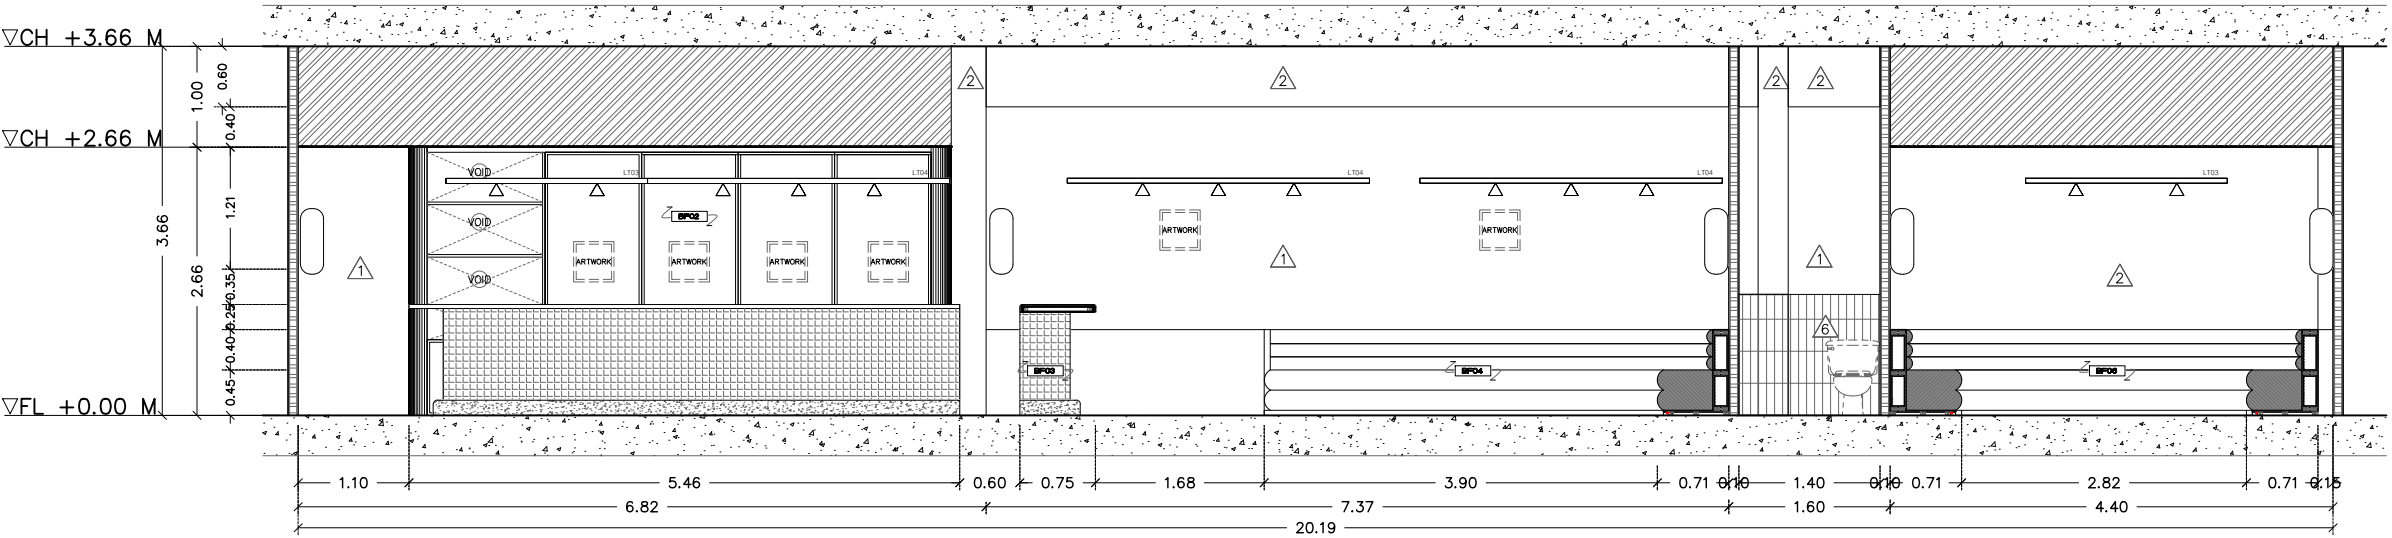

ELEVATION H

SCALE 1 : 75

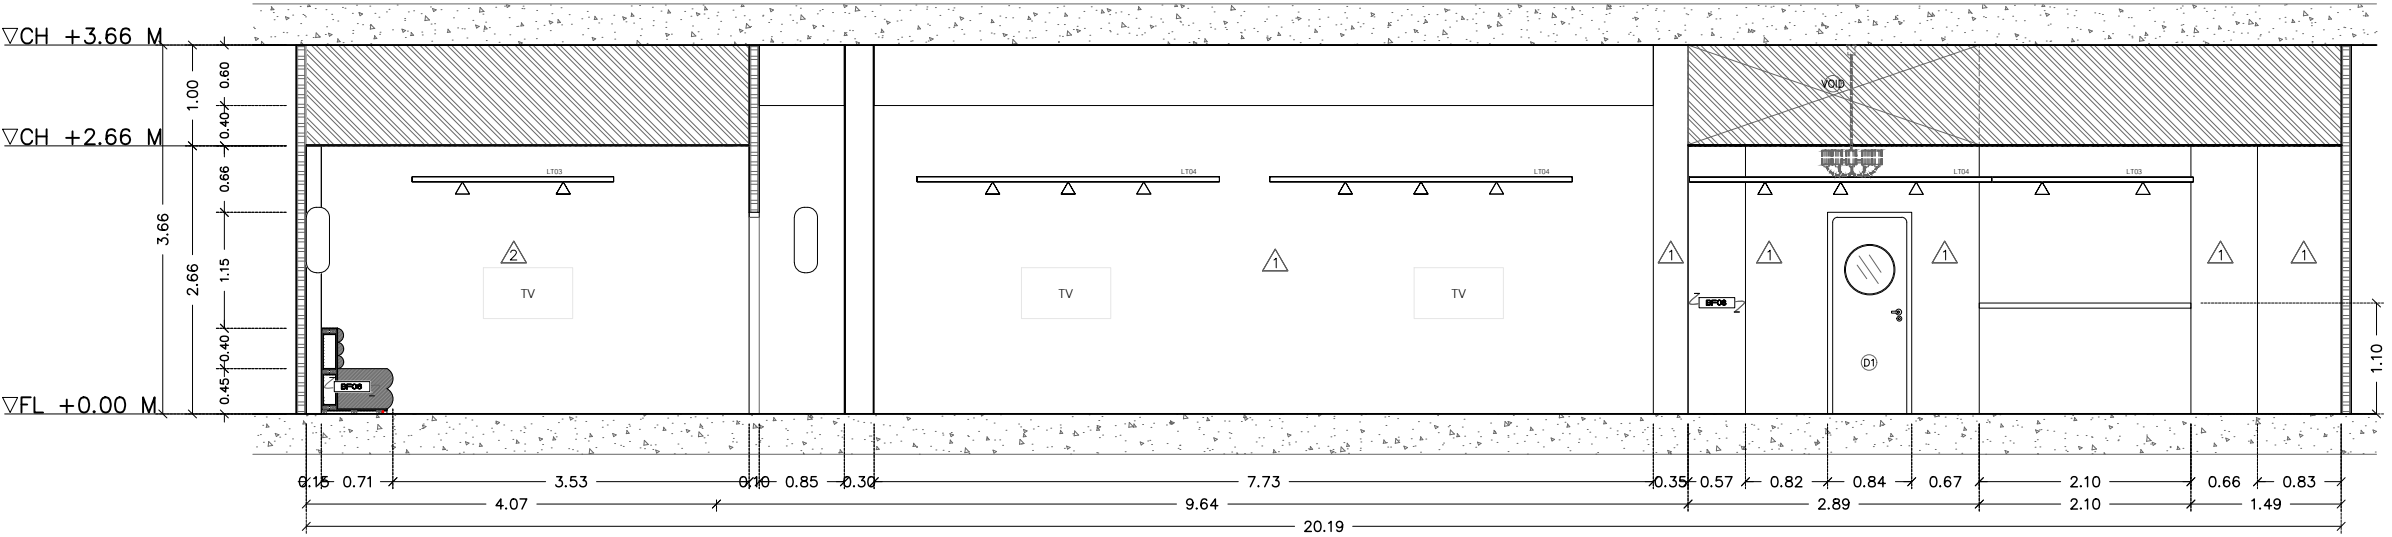

ELEVATION I

SCALE 1 : 75